


THIS SPOOL MARKUP DRAWING IS GENERATED FROM ENGINEERING PCF & REFERRING APPROVED ENGG ISOMETRICS. ENGINEERING ISOMETRICS TO BE REFERRED FOR REVISION APPROVAL INFORMATION & IN CASE OF ANY DISCREPANCY DATA GIVEN IN ENGINEERING ISOMETRIC SHALL GOVERN

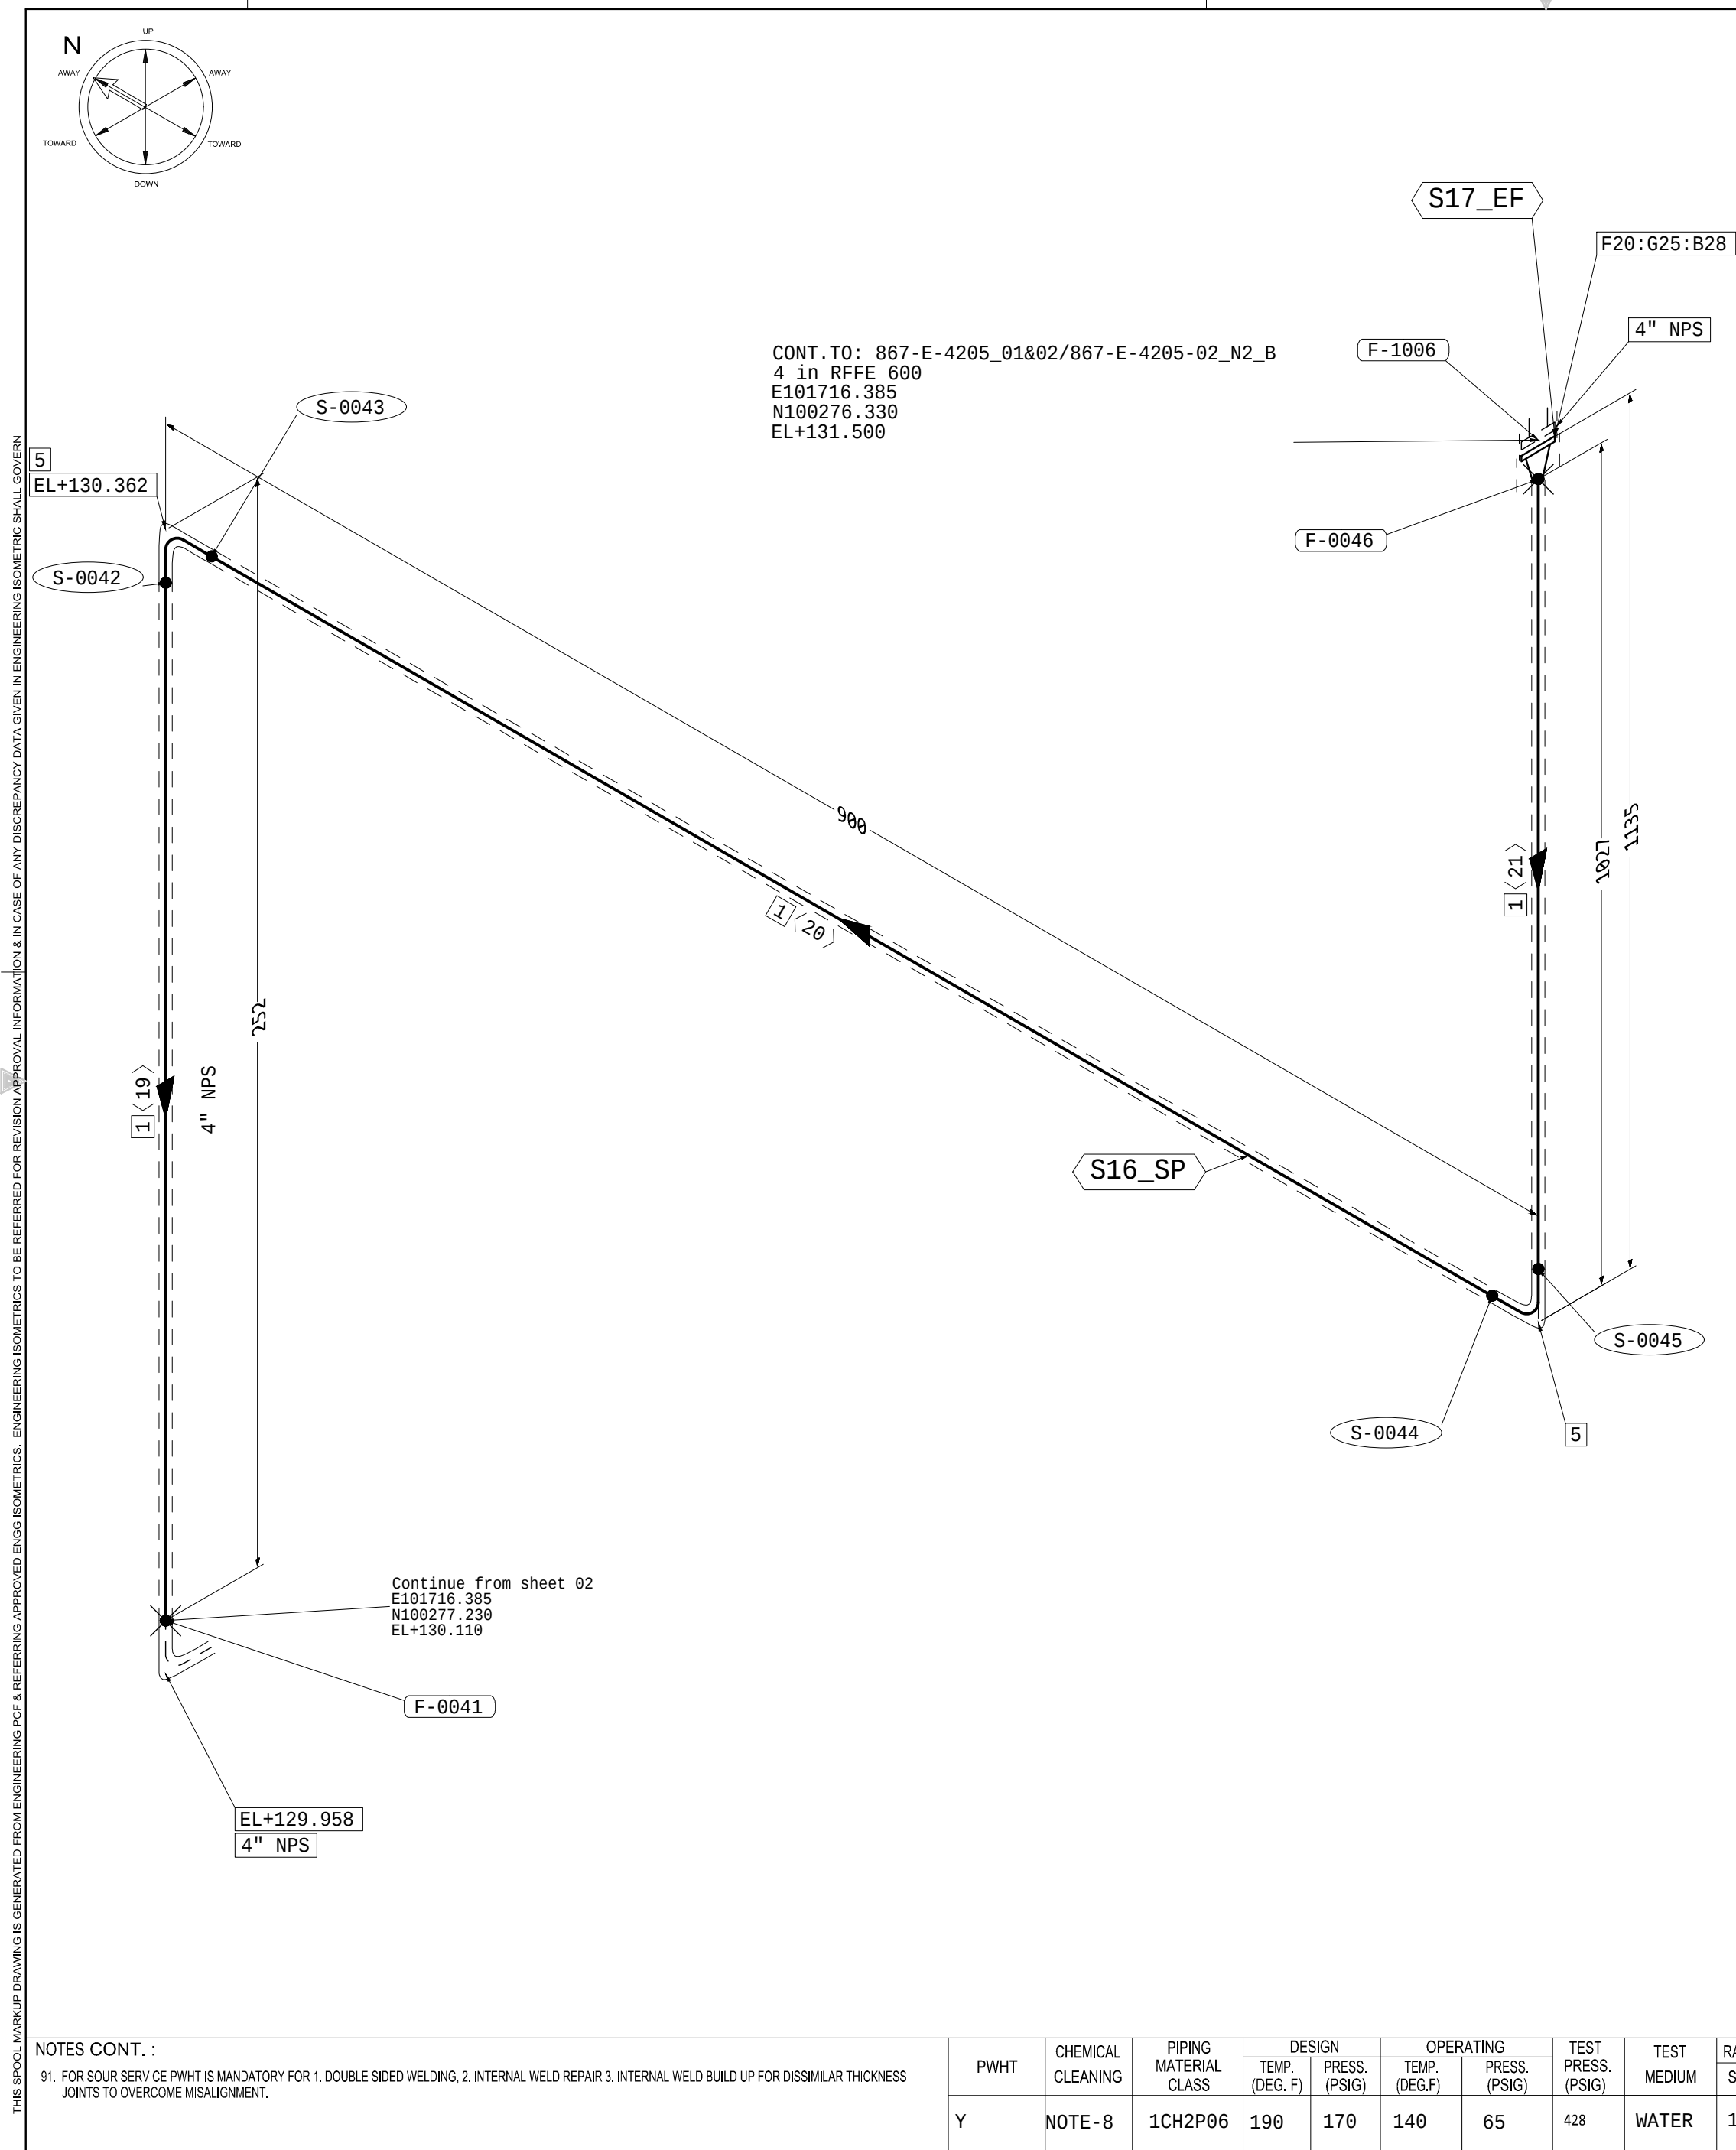

PT No.

DESCRIPTION

NPD(IN)

ITEM CODE

QTY

PIPES

1 PIPE SMLS 4" A106-B SOUR STD BE B36.10M

4 PPS2AERT04ZZABUAIA

1.571

FITTINGS

5 ELB 90° SMLS LR 4" A234-WPB SOUR STD BE B16.9

4 PE92AZRT04ZZABUAIQ

2

FLANGES

20 FLG WNR 4" A105N SOUR STD, 600# 125 B16.5

4 PFY2ADRT04ZZAEMADH

1

GASKET

25 GSK SPR WND W/CS CENTERING RING + I - SS 4" 4.50 MM THICK SS316L+GRPH FILL SOUR 600# B16.20

4 PGUUB5RT04AIAADZCC

1

FASTSNERS

28 BOLT, STUD+2 NUTS A193 GR B7M/ A194 GR 2HM, CERAMIC FLP COAT SOUR B18.2.1/18.2.2 - 160 mm Length

0.875 PH8ASCRTAH00160ZZF

8

STANDARD DETAIL REFERENCE DRAWINGS

DETAILS HEAVY WELDING BOSS FOR THREADED CONNECTIONS
CONSTRUCTION DETAILS AND DETAILS FOR ISOMETRIC PIPING
INSULATION DETAILS FOR HOT PIPING
INSTALLATION OF JACK SCREWS FOR FLANGED JOINTS

AE-036175
AD-036077
AA-036911
AA-036913
AC-036930

NOTES

1. MATERIAL SHOWN WITH A BROKEN LINE AND SPOOLS LISTED IN THE SAUDI ARAMCO FABRICATION LIST ARE NOT TO BE FURNISHED BY THE VENDOR.
2. PIPING DETAILS SHALL BE CUT AT ALL POINTS MARKED F.W. (FIELD WELD).
3. EACH FABRICATED SECTION SHALL BE CLEARLY MARKED WITH ITS CODE NUMBER.
4. UNLESS OTHERWISE NOTED: (A) ALL DIMENSIONS ARE TO FACE OF FLANGES, (B) BOLT HOLES ON FLANGES STRADDLE C. (C) WELDING ELBOWS ARE LONG RADIUS.
5. FABRICATION SHALL BE IN ACCORDANCE WITH SAUDI ARAMCO SPECIFICATION 01-SAMSS-10.
6. GASKET ALLOWANCE
7. PIPING MATERIAL IS

PIPE SIZE SCHEDULE SPECIFICATION

WELDING STRESS RELIEF - YES NO SPOT X-RAY 01-SAMSS-10 100% X-RAY TESTING SHOP HYDROSTATIC TEST - YES THE SHOP HYDROSTATIC TEST SHALL BE CARRIED OUT ON PIECES HAVING ALL ENDS FLANGED, HYDROSTATIC TEST PRESSURE, ALL PIPING MATERIAL IS IN ACCORDANCE WITH SAUDI ARAMCO ENGINEERING SPECIFICATION SAES-L-105 CLASS ALL EXCEPTIONS ARE NOTED ON THE ISOMETRIC. INSULATION REQUIRED - YES NO INSULATION SHOWN ON DRAWING

SPOOLS TO BE FABRICATED BY VENDOR

SPOOLS TO BE FABRICATED BY SAUDI ARAMCO

REFERENCE DRAWINGS

PIPING PLAN YA-212287
P&ID NO. YA-221177-001
PLOT PLAN KEY PLAN NO. YA-212083
INDEX FOR PIPING ISO (AG) PP-867-LI-0003
INDEX FOR PIPING ISO (UG) PP-867-LI-0004

00A 02-05-25 ISSUED FOR CONSTRUCTION AC/SN KY/PD BSP HJ
REV DATE PREP BY CHK BY APP BY APP BY

REVISION STATUS

REVISION VALIDATION

THIS REVISION NO. 00A IS COVERED FOR ALL APPROVAL AND CERTIFICATION REQUIREMENTS. PER SAEP-33A UNDER DRAWING COMPLETION CERTIFICATE NO. 10-14815-0003-000

DESIGN CERTIFICATION (DESIGN AGENCY) REVIEW FOR KEY DRAWINGS (SAUDI ARAMCO) OTHER

ENGL DATE CERTIFIED BY DATE CONT. AGENCY DATE OPERATIONS DATE BY DATE

REV NO. DATE REVISION DESCRIPTION

JOB ORDER/REV NO. 10-14815-0003 THIS REVISION IS NOT TO BE USED FOR CONSTRUCTION UNLESS CERTIFIED AND DATED

SAUDI ARABIAN OIL COMPANY

ISOM 8" - MDEA-17356-1CH2P06 DRAWING TYPE ISO

MDEA SERVICE

JFGP GAS PROCESSING TRAIN-4

JAFURAH SAUDI ARABIA

PLANT NO. INDEX DRAWING NUMBER SHT. NO. REV. NO.

867 L YB-215331 070f07 00A

SITE REV. NO. 00A

RESTRICTED SMART

CADD-03

PIPE CUT LENGTH SUMMARY

SPL No. NPD PC No. LENGTH ALLOWANCE TOTAL LENGTH

S16_SP 4 <19> 0.100 0.000 0.100

S16_SP 4 <20> 0.596 0.000 0.596

S16_SP 4 <21> 0.875 0.000 0.875

ISO For

NOTES :
1. ALL COORDINATES AND ELEVATIONS ARE IN 'METER' AND ALL DIMENSIONS ARE IN 'MM'.
2. PIPE QUANTITY IS IN METERS AND OTHER QUANTITY IN NUMBERS.
3. FOR STANDARD SUPPORT, REFER DOC. NO. "PP-866-ST-0001".
4. IN CASE OF ANY DISCREPANCY FOR LINE CONDITIONS, LINE DATA GIVEN IN LINE LIST SHALL GOVERN
5. FOR SMALL BORE LINES, DIMENSION & ROUTING SHALL BE FIELD ADJUSTED.
6. THE SPECIFIED THEORETICAL LOCATION OF EQUIPMENT NOZZLES, SUPPORTING STRUCTURE SHALL BE VERIFIED BEFORE INSTALLING THE PIPING & INTOLERABLE DISCREPANCIES SHALL BE DISCUSSED WITH DESIGN SITE ENGINEER.
7. ALL THREADED CONNECTION SHALL BE SEAL WELDED, EXCEPT DRAIN AND VENT PLUG.
8. REFER LINE LIST.
9. ALL PRESSURE WELDS, OTHER THAN BUTT WELDS, INCLUDING BRANCH CONNECTIONS SUCH AS BRANCH-OLETS, AND BOSS) SHALL BE 100% PT/MT EXAMINED. ALL ATTACHMENT WELDS ON PRESSURIZED COMPONENTS THAT ARE NOT HYDROTESTED AFTER MAKING THE ATTACHMENT WELD SHALL BE 100% PT/MT EXAMINED.

BUTT WELD FIELD WELD
INSULATED PIPE TRACED PIPE
PIPE SUPPORT PLATFORM PENETRATION
SOCKET WELD SCREWED JOINT