


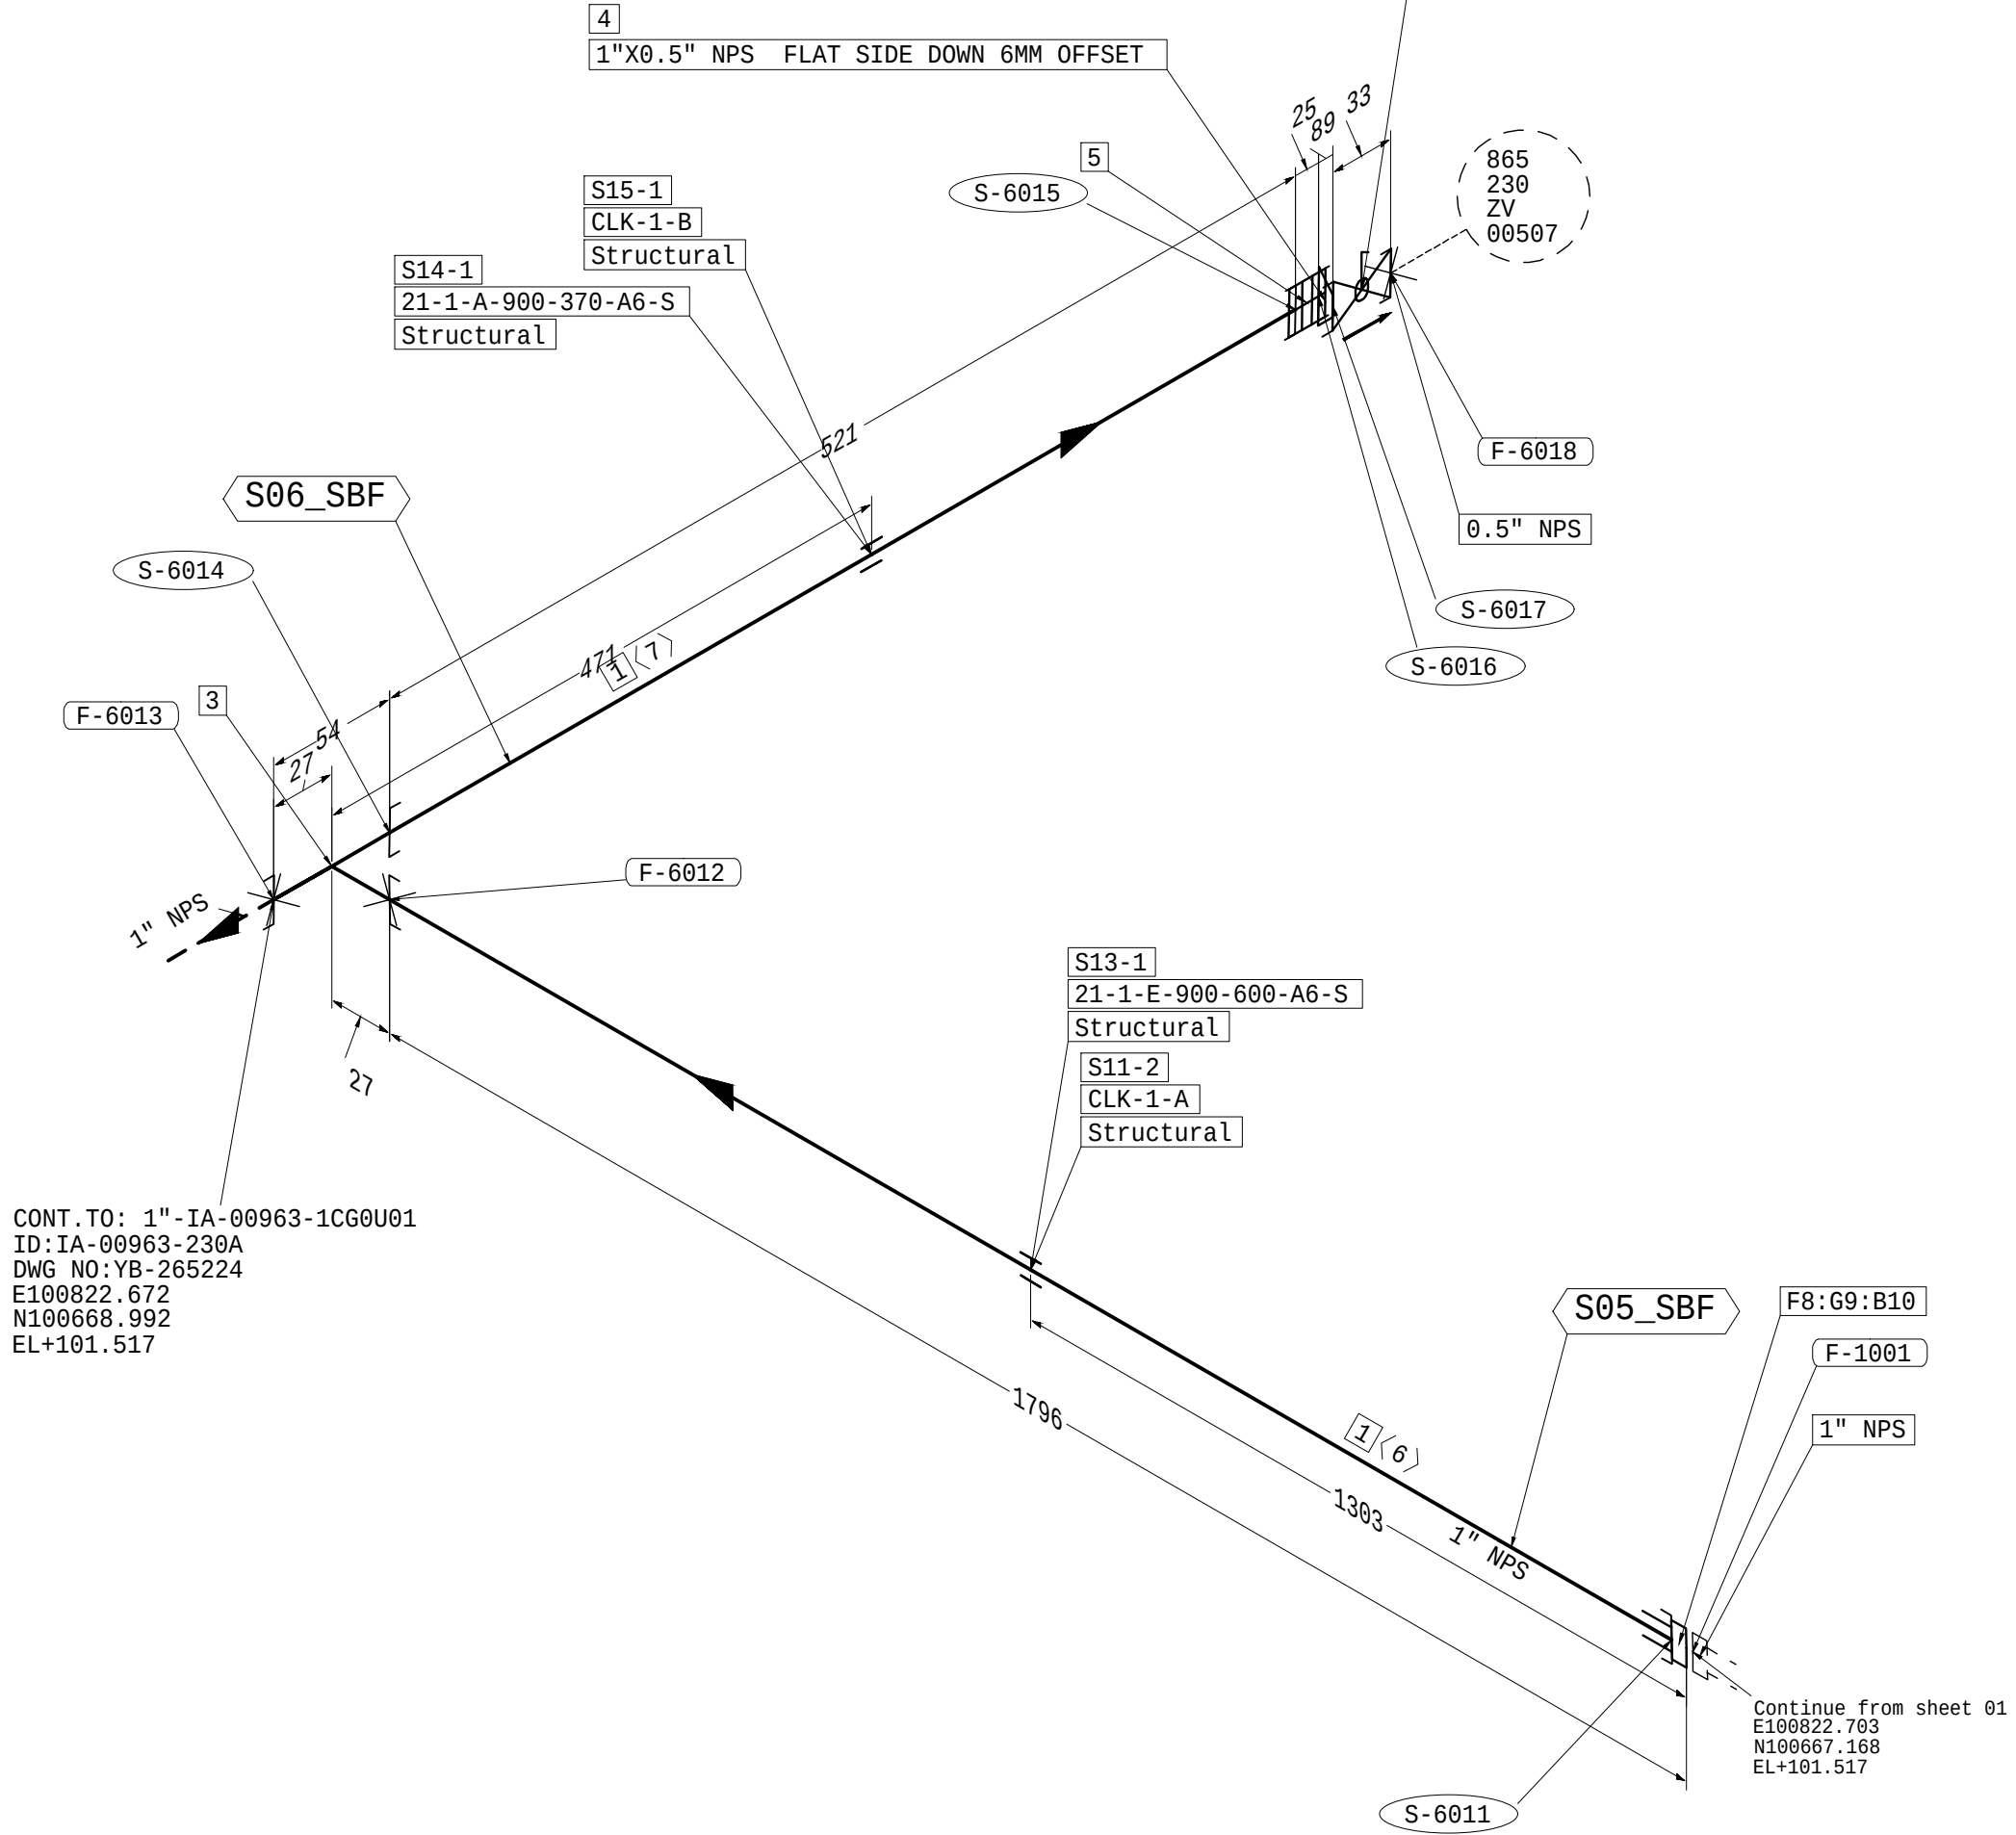

Continue from sheet 01
E100822.703
N100667.168
EL+101.517

PWH#	CHEMICAL CLEANING	PIPING MATERIAL CLASS	DESIGN		OPERATING		TEST PRESS. (PSIG)	TEST MEDIUM	RADIOGRAPHY %		INSULATION		TRACING	PAINTING	STRESS SYS NO.	LINE ID
			TEMP. (DEG. F)	PRESS. (PSIG)	TEMP. (DEG.F)	PRESS. (PSIG)			SHOP	FIELD	THK (MM)	TYPE				
N	NOTE - 8	1C60U01	185	145	135	125	125	SERVICE	NA	NA	0	NI	NA	APCS-26		IA-00910-230A

NOTES : 1. ALL COORDINATES AND ELEVATIONS ARE IN 'METER' AND ALL DIMENSIONS ARE IN 'MM'. 2. PIPE QUANTITY IS IN METERS AND OTHER QUANTITY IN NUMBERS. 3. FOR STANDARD SUPPORT, REFER DOC. NO. "PP-866-S2-0001". 4. IN CASE OF ANY DISCREPANCY FOR LINE CONDITIONS, LINE DATA GIVEN IN LINE LIST SHALL GOVERN 5. FOR SMALL BORE LINES, DIMENSION & ROUTING SHALL BE FIELD ADJUSTED. 6. THE SPECIFIED THEORETICAL LOCATION OF EQUIPMENT NOZZLES, SUPPORTING STRUCTURE SHALL BE VERIFIED BEFORE INSTALLING THE PIPING & INTOLERABLE DISCREPANCES SHALL BE DISCUSSED WITH DESIGN SITE ENGINEER. 7. ALL THREADED CONNECTION SHALL BE SEAL WELDED, EXCEPT BRAIN AND VENT PLUG. 8. REFER LINE LIST. 9. ALL PRESSURE WELDS, OTHER THAN BUTT WELDS, INCLUDING BRANCH CONNECTIONS SUCH AS BRANCH-OLETS, AND BOSS) SHALL BE 100% PT/MT EXAMINED. ALL ATTACHMENT WELDS ON PRESSURIZED COMPONENTS THAT ARE NOT HYDROTESTED AFTER MAKING THE ATTACHMENT	<table border="0"> <tr> <td></td> <td></td> </tr> <tr> <td>BUTT WELD</td> <td>FIELD WELD</td> </tr> <tr> <td></td> <td></td> </tr> <tr> <td>INSULATED PIPE</td> <td>TRACED PIPE</td> </tr> <tr> <td></td> <td></td> </tr> <tr> <td>PIPE SUPPORT</td> <td>PLATFORM PENETRATION</td> </tr> <tr> <td></td> <td></td> </tr> <tr> <td>SOCKET WELD</td> <td>SCREWED JOINT</td> </tr> </table>			BUTT WELD	FIELD WELD			INSULATED PIPE	TRACED PIPE			PIPE SUPPORT	PLATFORM PENETRATION			SOCKET WELD	SCREWED JOINT
																	
BUTT WELD	FIELD WELD																
																	
INSULATED PIPE	TRACED PIPE																
																	
PIPE SUPPORT	PLATFORM PENETRATION																
																	
SOCKET WELD	SCREWED JOINT																

THIS DRAWING AND THE INFORMATION CONTAINED HEREIN ARE THE SOLE PROPERTY OF SAUDI ARAMCO. NO REPRODUCTION IN FULL, OR IN PART, SHALL BE OBTAINED FROM THIS DRAWING WITHOUT THE WRITTEN CONSENT OF SAUDI ARAMCO.