


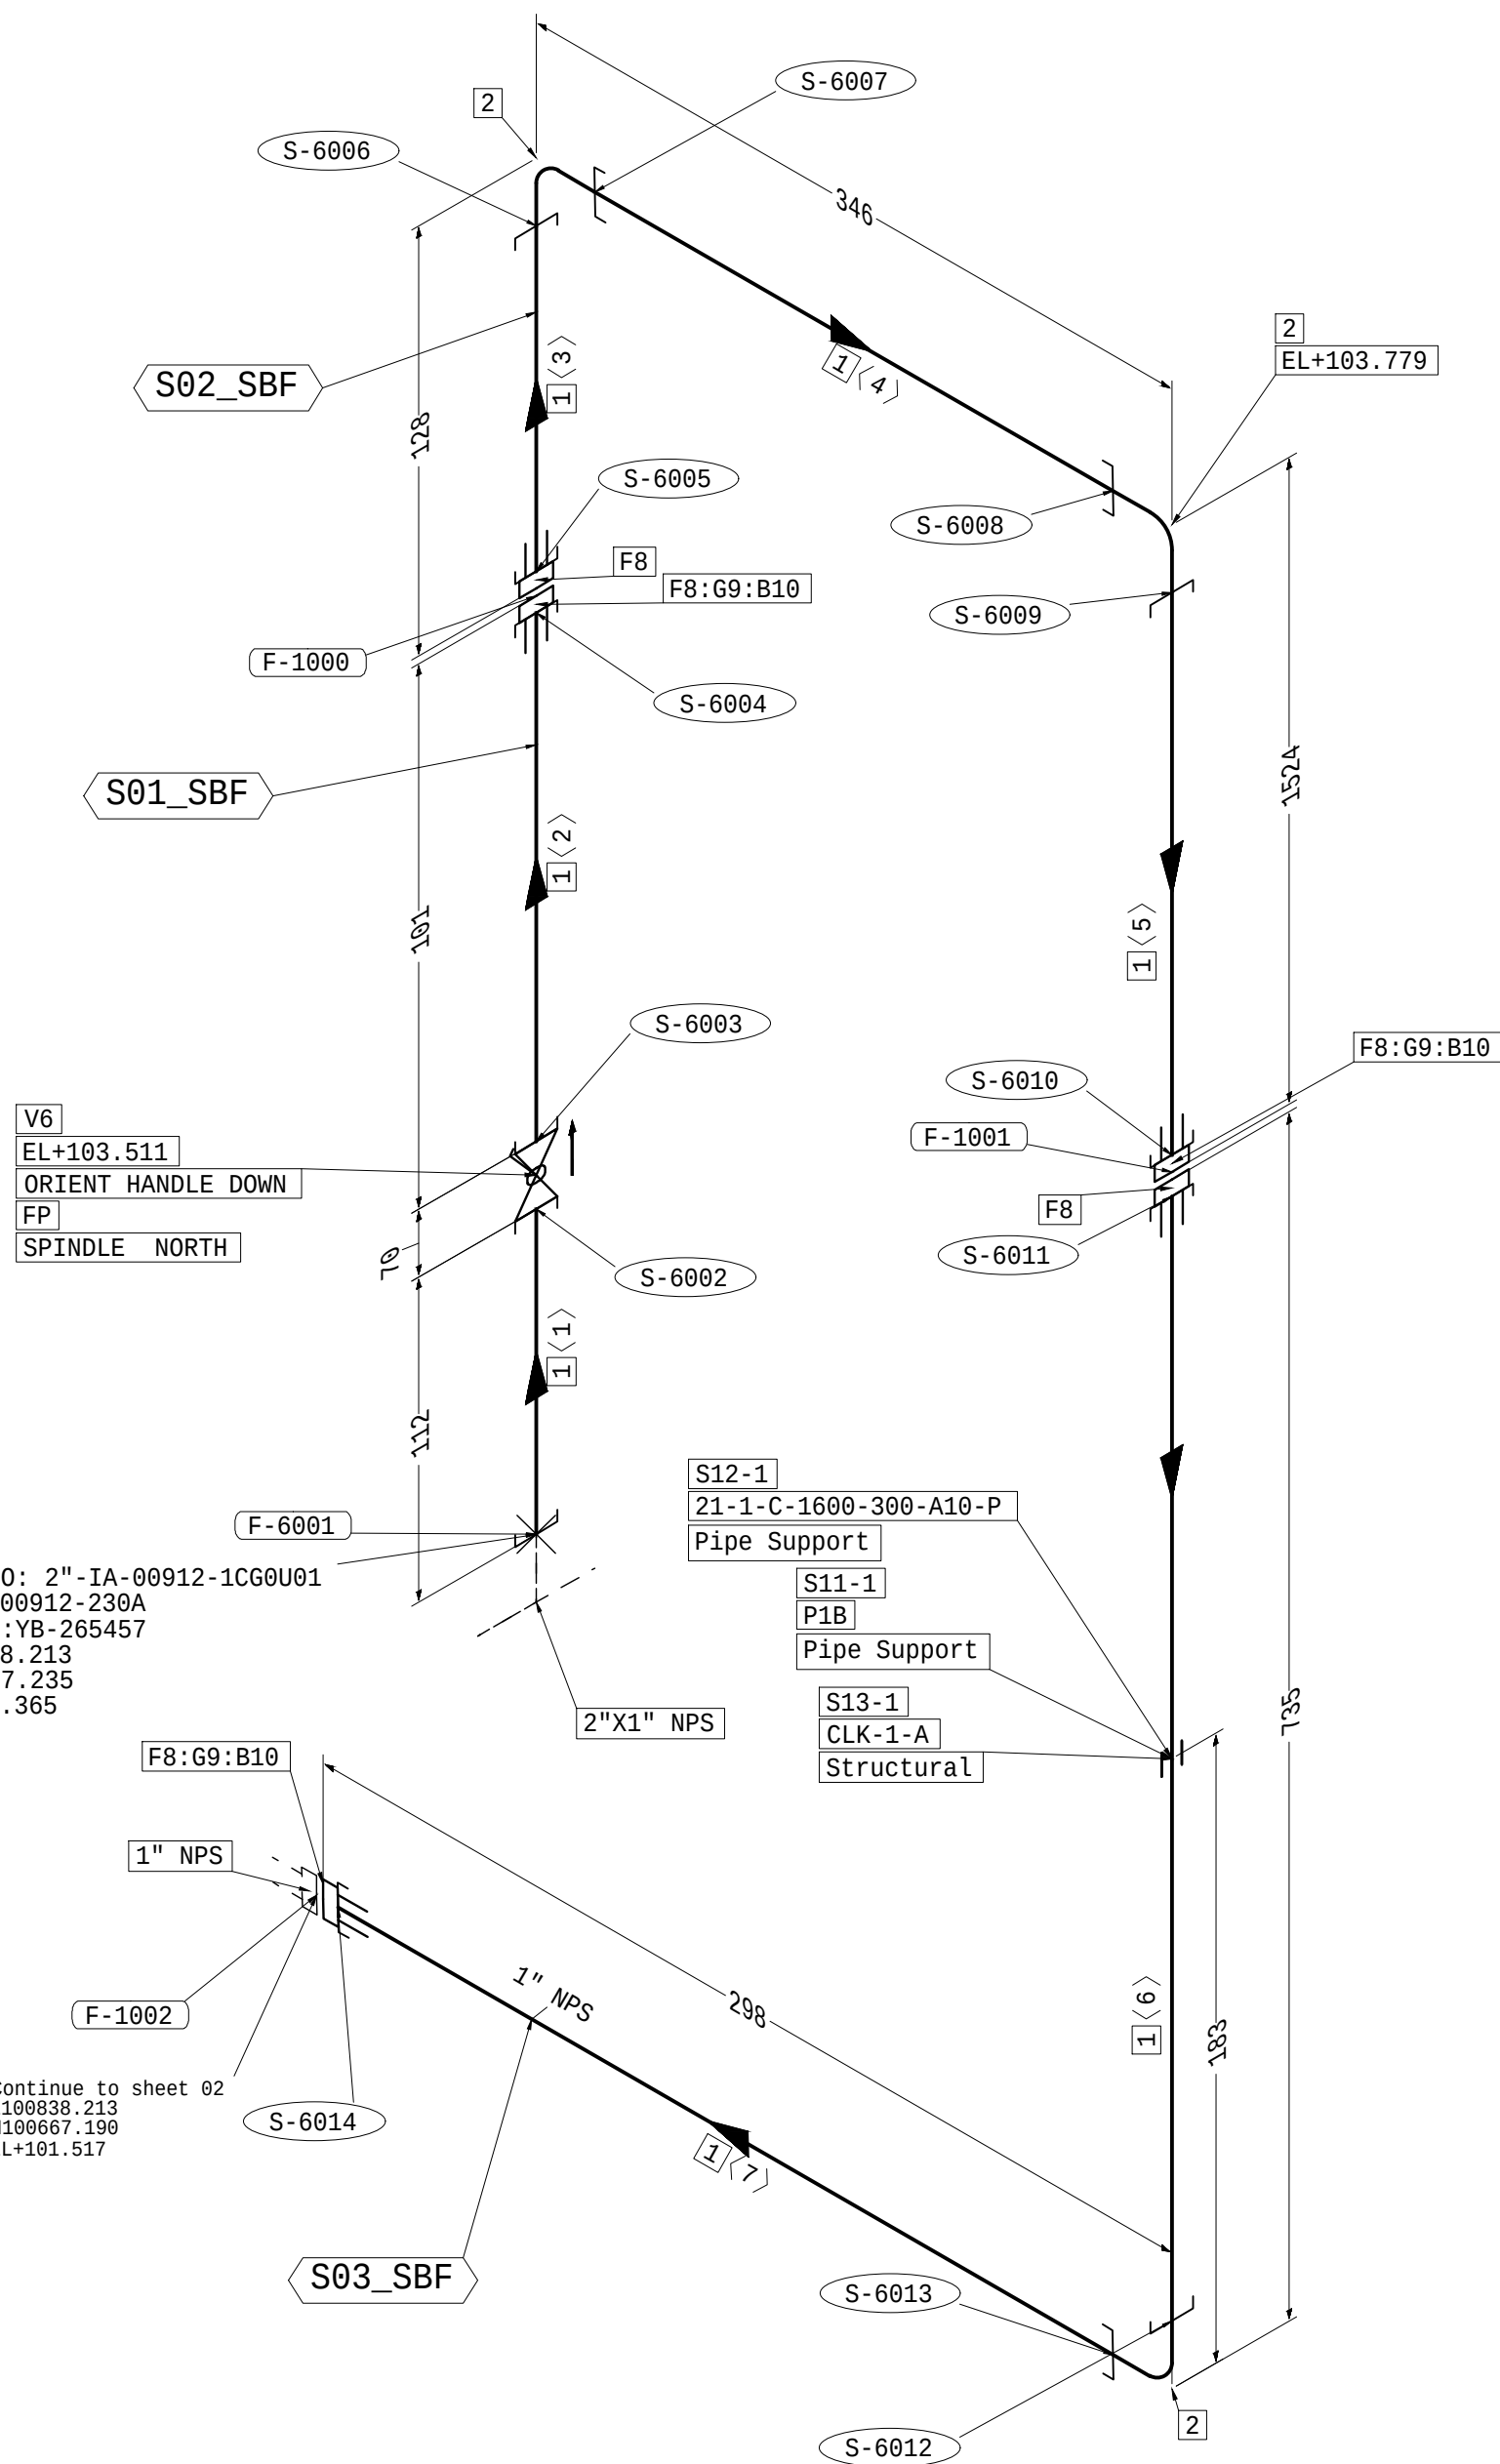

NOTES CONT. :

91. FOR SOUR SERVICE PWHT IS MANDATORY FOR 1. DOUBLE SIDED WELDING, 2. INTERNAL WELD REPAIR 3. INTERNAL WELD BUILD UP FOR DISSIMILAR THICKNESS JOINTS TO OVERCOME MISALIGNMENT.

450390	13-02-2026
450444	21-04-2026

NOTES :	BUTT WELD	FIELD WELD
1. ALL COORDINATES AND ELEVATIONS ARE IN 'METER' AND ALL DIMENSIONS ARE IN 'MM'.		
2. PIPE QUANTITY IS IN METERS AND OTHER QUANTITY IN NUMBERS.	INSULATED PIPE	TRACED PIPE
3. FOR STANDARD SUPPORT, REFER CODE NO. "PP-866-S2-0001".		
4. IN CASE OF ANY DISCREPANCY FOR LINE CONDITIONS, LINE DATA GIVEN IN LINE LIST SHALL GOVERN		
5. FOR SMALL BORE LINES, DIMENSION & ROUTING SHALL BE FIELD ADJUSTED.		
6. THE SPECIFIED THEORETICAL LOCATION OF EQUIPMENT NOZZLES, SUPPORTING STRUCTURE SHALL BE VERIFIED BEFORE INSTALLING THE PIPING & INTOLERABLE DISCREPANCIES SHALL BE DISCUSSED WITH DESIGN SITE ENGINEER.		
7. THE ABOVE CONNECTION - SHD BE SEAL WELDED, EXCEPT DRAIN AND VENT PLUG -		
8. REFER LINE LIST.		
9. ALL PRESSURE WELDS, OTHER THAN BUTT WELDS, INCLUDING BRANCH CONNECTIONS SUCH AS BRANCH-OLETS, AND BOSS) SHALL BE 100% PT/MT EXAMINED. ALL ATTACHMENT WELDS ON PRESSURIZED COMPONENTS THAT ARE NOT HYDROTESTED AFTER MAKING THE ATTACHMENT		
10. 100% PT/MT EXAMINATION		
	PIPE SUPPORT	PLATFORM PENETRATION
		
	SOCKET WELD	SCREWED JOINT
		

[illegible]

THIS DRAWING AND THE INFORMATION CONTAINED HEREIN ARE THE SOLE PROPERTY OF SAUDI ARAMCO. NO REPRODUCTION IN FULL, OR IN PART, SHALL BE OBTAINED FROM THIS DRAWING WITHOUT THE WRITTEN CONSENT OF SAUDI ARAMCO.