
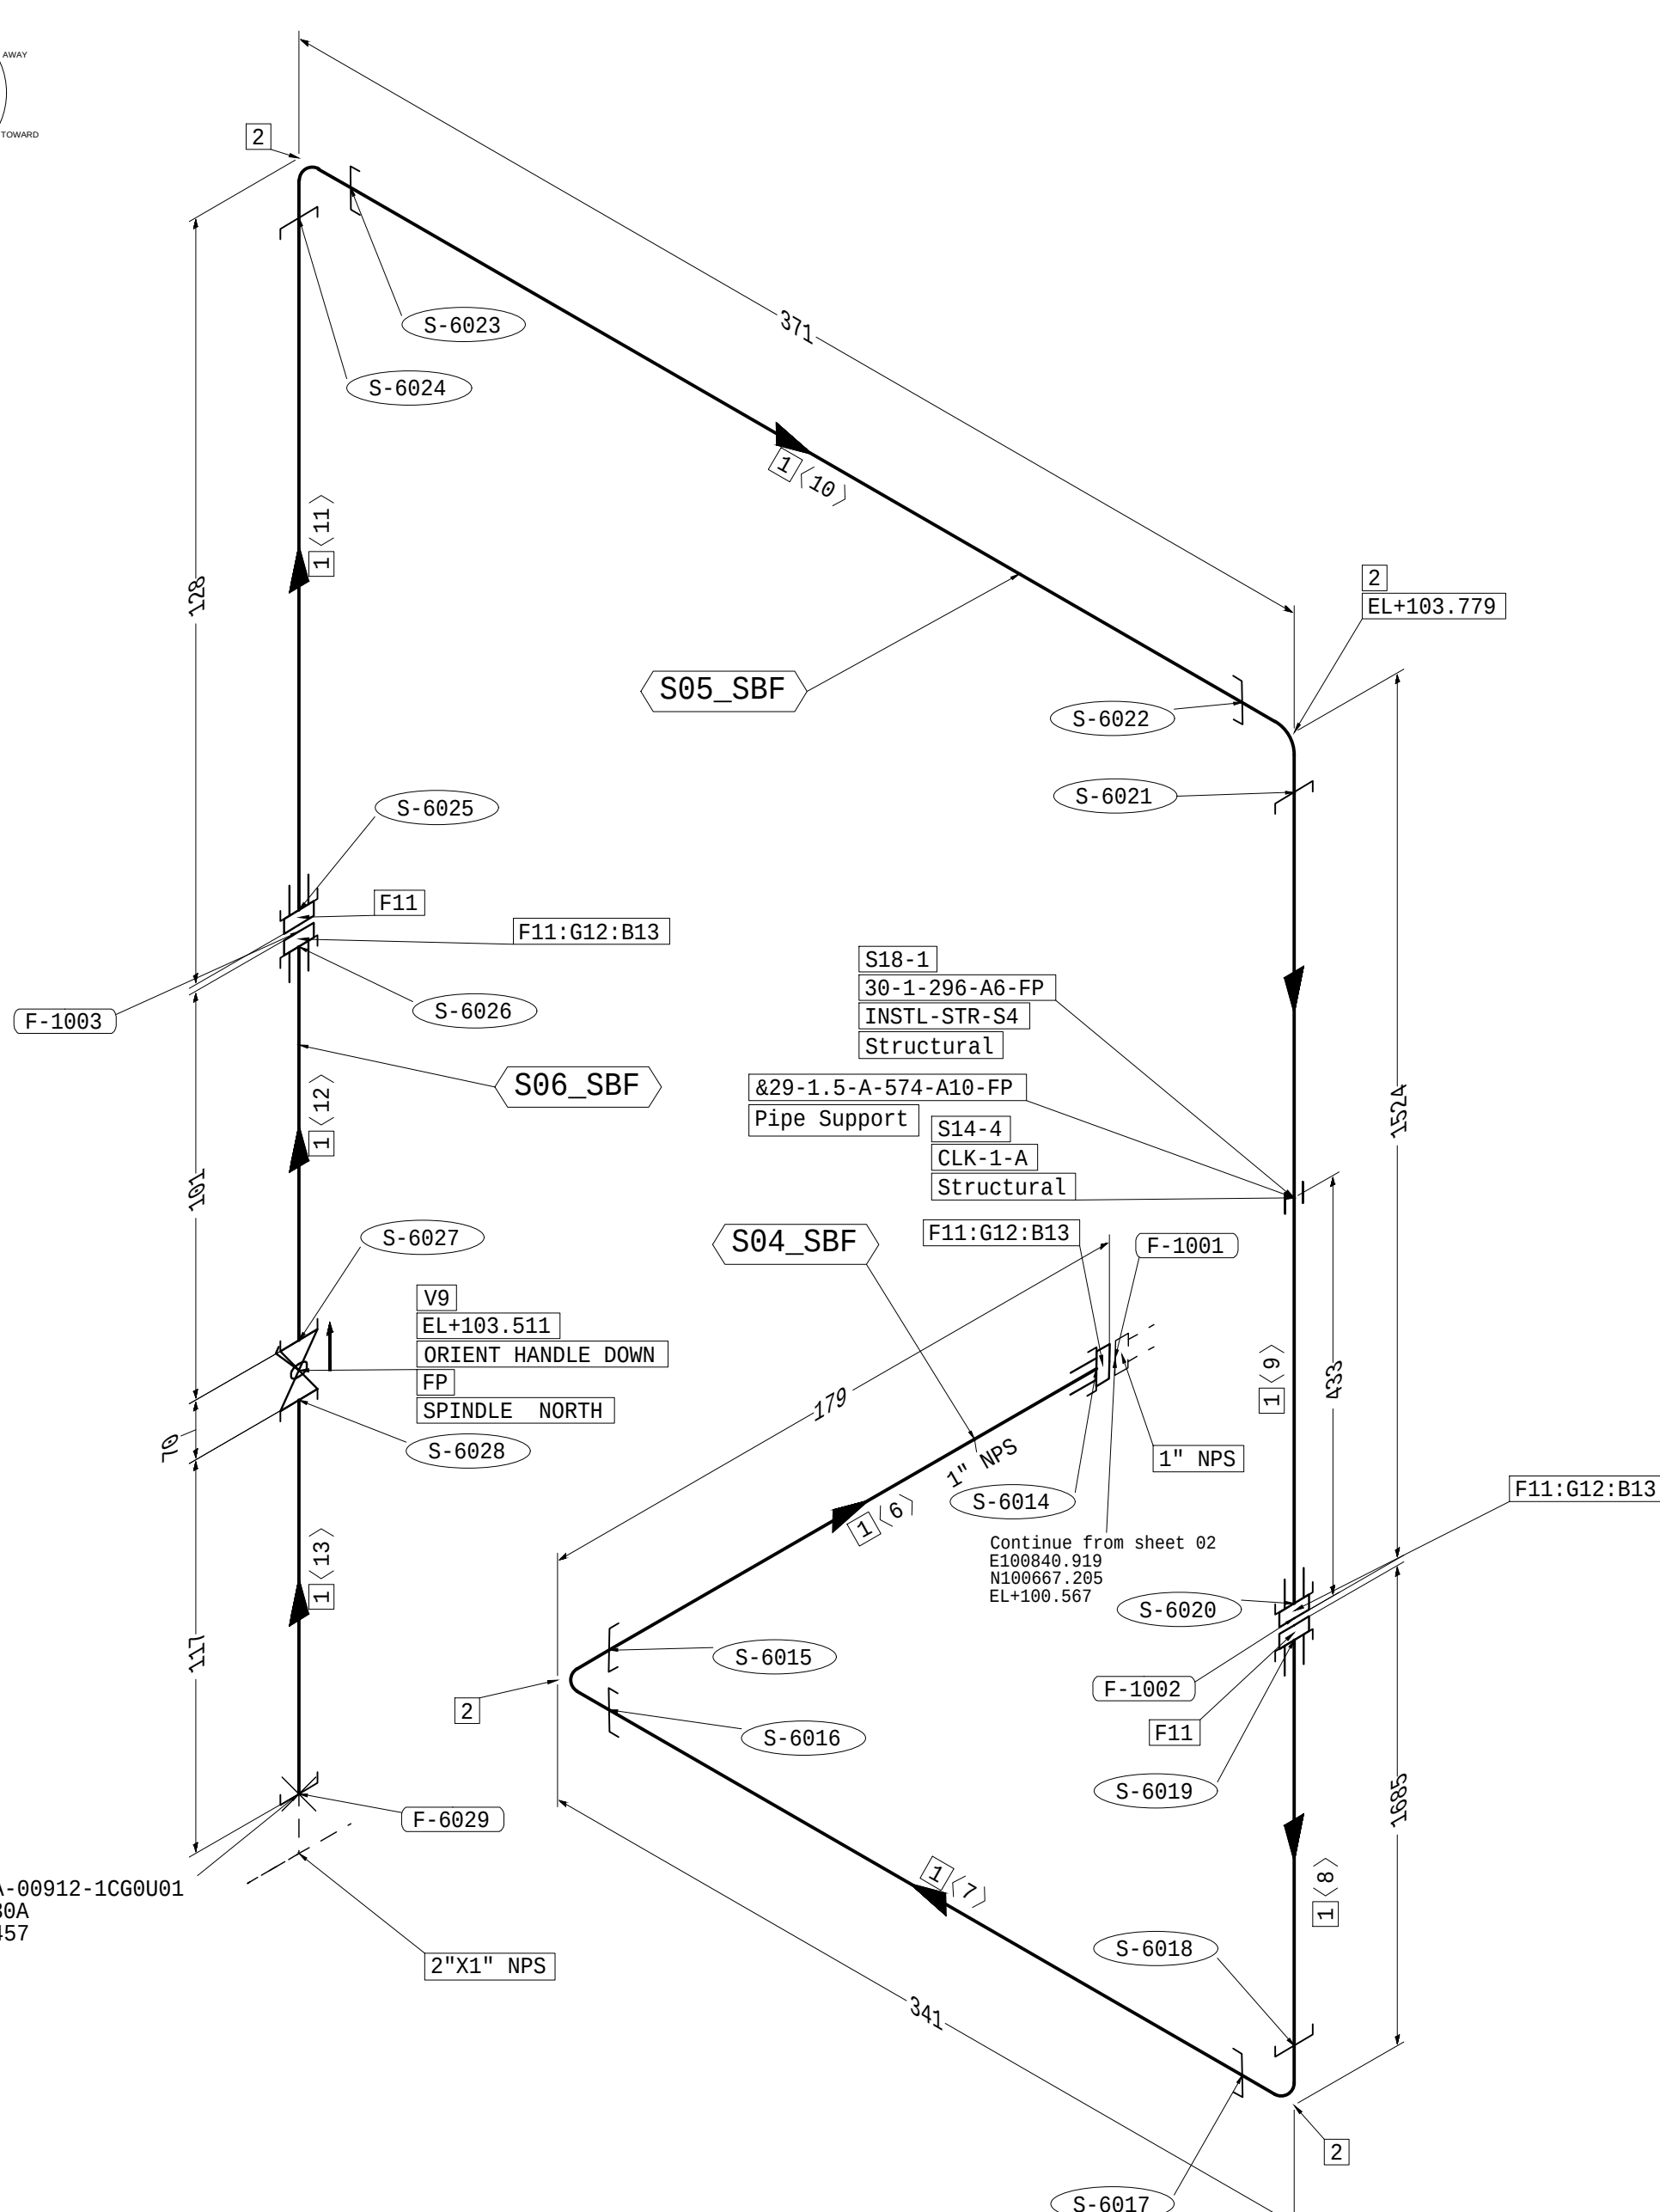


THIS SPOOL MARKUP DRAWING IS GENERATED FROM ENGINEERING P&ID & REFERRING APPROVED ENGG ISOMETRICS. ENGINEERING ISOMETRICS TO BE REFERRED FOR REVISION APPROVAL INFORMATION & IN CASE OF ANY DISCREPANCY DATA GIVEN IN ENGINEERING ISOMETRIC SHALL GOVERN

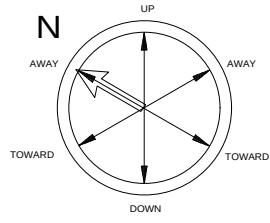

CONT.TO: 2"-IA-00912-1CG0U01
ID:IA-00912-230A
DWG NO:YB-265457
E100840.737
N100667.235
EL+103.359

All Pipe attached supports shall be welded before galvanising.

MATERIALS					STANDARD DETAIL REFERENCE DRAWINGS				
PT No.	DESCRIPTION	NPD(IN)	ITEM CODE	QTY	DETAILS HEAVY WELDING ROSSSES FOR THREADED CONNECTIONS CONSTRUCTION DETAILS AND DETAILS FOR ISOMETRIC PIPING INSULATION DETAILS FOR HOT PIPING INSULATION DETAILS FOR COLD PIPING INSTALLATION OF JACK SCREWS FOR FLANGED JOINTS				
PIPES					AE-036175 AD-036177 AA-036181 AC-036183				
1	PIPE SMLS 1" A106-B GALV STD NPT (M) B36.10M	1	PPS2AEAE01ZZABUUA	4.231					
FITTINGS									
2	ELB 90° FRG LR 1" A105N GALV 3000# NPT (F) B16.11	1	PE72ADAE01ZZAA0ATA	4					
VALVE									
9	TAG NO V0B-29-01-AS-AF-AA-BFI BALL VAL FB MSS-SP-110 1" B61/B62 BRONZE TRIM WITH RTFE SEAT 2/3 PIECE CONST,FLT TYP NPTF 150# LEVER OPT	1	V0B290I01ASAFABFI	1					
FLANGES									
11	FLG SCRD RF 1" A105N GALV 150# 125 B16.5	1	PFH2ADAE01ZZAAAADH	5					
GASKET									
12	GSK SPR WND W/CS CENTERING RING + I - SS 1" 4.50 MM THICK SS316L+GRPH FILL 150# B16.20	1	PGUUB5AG01AIAAAZZC	3					
FASTSNERS									
13	BOLT, STUD+2 NUTS A193 B7/ A194 2H, CERAMIC FLP COAT B18.2.1/18.2.2 - 80 mm Length	0.5	PH8AB5AGAE00080ZZF	12					
SUPPORTS									
14	PIPE SUPPORT	1	CLK-1-A	1					
18	PIPE SUPPORT	1	30-1-296-A6-FP	1					
NOTES					1. MATERIAL SHOWN WITH A BROKEN LINE AND SPOOLS LISTED IN THE SAUDI ARAMCO FABRICATION LIST ARE NOT TO BE FURNISHED BY THE VENDOR. 2. PIPING DETAILS SHALL BE CUT AT ALL POINTS MARKED F.W. (FIELD WELD). 3. EACH FABRICATED SECTION SHALL BE CLEARLY MARKED WITH ITS CODE NUMBER. 4. UNLESS OTHERWISE NOTED: (A) ALL DIMENSIONS ARE TO FACE OF FLANGES. (B) BOLT HOLES ON FLANGES STRADDLE C. (C) WELDING ELBOWS ARE LONG RADIUS. 5. FABRICATION SHALL BE IN ACCORDANCE WITH SAUDI ARAMCO SPECIFICATION 01-SAMSS-10. 6. GASKET ALLOWANCE 7. PIPING MATERIAL IS				
					PIPE SIZE SCHEDULE SPECIFICATION				
					8. WELDING STRESS RELIEF - YES ☐ NO ☐ 100% X-RAY ☐ SPOT X-RAY 01-SAMSS-10 ☐				
					9. TESTING SHOP HYDROSTATIC TEST - YES ☐ NO ☐ THE SHOP HYDROSTATIC TEST SHALL BE CARRIED OUT ON PIECES HAVING ALL ENDS FLANGED. HYDROSTATIC TEST PRESSURE				
					10. ALL PIPING MATERIAL IS IN ACCORDANCE WITH SAUDI ARAMCO ENGINEERING SPECIFICATION SAES-L-105 CLASS . ALL EXCEPTIONS ARE NOTED ON THE ISOMETRIC.				
					11. INSULATION REQUIRED - YES ☐ NO ☐ INSULATION SHOWN ON DRAWING				
					SPOOLS TO BE FABRICATED BY VENDOR				
					NO. MARK NO. SIZE WEIGHT NO. MARK NO. SIZE WEIGHT PIECES PIECES LBS PIECES LBS				
					SPOOLS TO BE FABRICATED BY SAUDI ARAMCO				
					NO. MARK NO. SIZE NO. MARK NO. SIZE PIECES PIECES LBS PIECES LBS				
					REFERENCE DRAWINGS				
					PIPING PLAN				
					P&ID NO. YA-221234-001				
					PLOT PLAN KEY PLAN NO. TA-293108				
					INDEX FOR PIPING ISO (AG) PP-865-LI-0003				
					INDEX FOR PIPING ISO (UG) PP-865-LI-0004				
					REV DATE DESCRIPTION PREP BY CHKD BY APP BY HJ				
					REVISION STATUS				
					REVISION VALIDATION				
					THIS REVISION NO. 00 IS COVERED, FOR ALL APPROVAL AND CERTIFICATION REQUIREMENTS, PER SAEP-33A, UNDER DRAWING COMPLETION CERTIFICATE NO: 10-14815-0003-000				
					DESIGN CERTIFICATION (DESIGN AGENCY) REVIEW FOR KEY DRAWINGS (SAUDI ARAMCO) OTHER				
					ENGG. DATE CERTIFIED BY DATE COST AGENCY DATE OPERATIONS DATE BY DATE				
					REV. NO. DATE REVISION DESCRIPTION				
					JOB ORDER/REV. NO. THIS REVISION IS NOT TO BE USED FOR CONSTRUCTION UNLESS CERTIFIED AND SIGNED				
					10-14815-0003				
					SAUDI ARABIAN OIL COMPANY				
					ISOM 1" -IA-00969-1CG0U01 ISO				
					IA SERVICE				
					JFGP GAS PROCESSING TRAIN-2				
					JAFURAH SAUDI ARABIA				
					PLANT NO. INDEX DRAWING NUMBER SHT. NO. REV. NO.				
					865 L YB-265229 030f03 00				
					SITE REV. NO. 001 RESTRICTED SMART CADD-03				

450390 13-02-2026
450444 21-04-2026