


THIS SPOOL MARKUP DRAWING IS GENERATED FROM ENGINEERING PDF & REFERRING APPROVED ENGG ISOMETRICS. ENGINEERING ISOMETRICS TO BE REFERRED FOR REVISION APPROVAL INFORMATION & IN CASE OF ANY DISCREPANCY DATA GIVEN IN ENGINEERING ISOMETRIC SHALL GOVERN

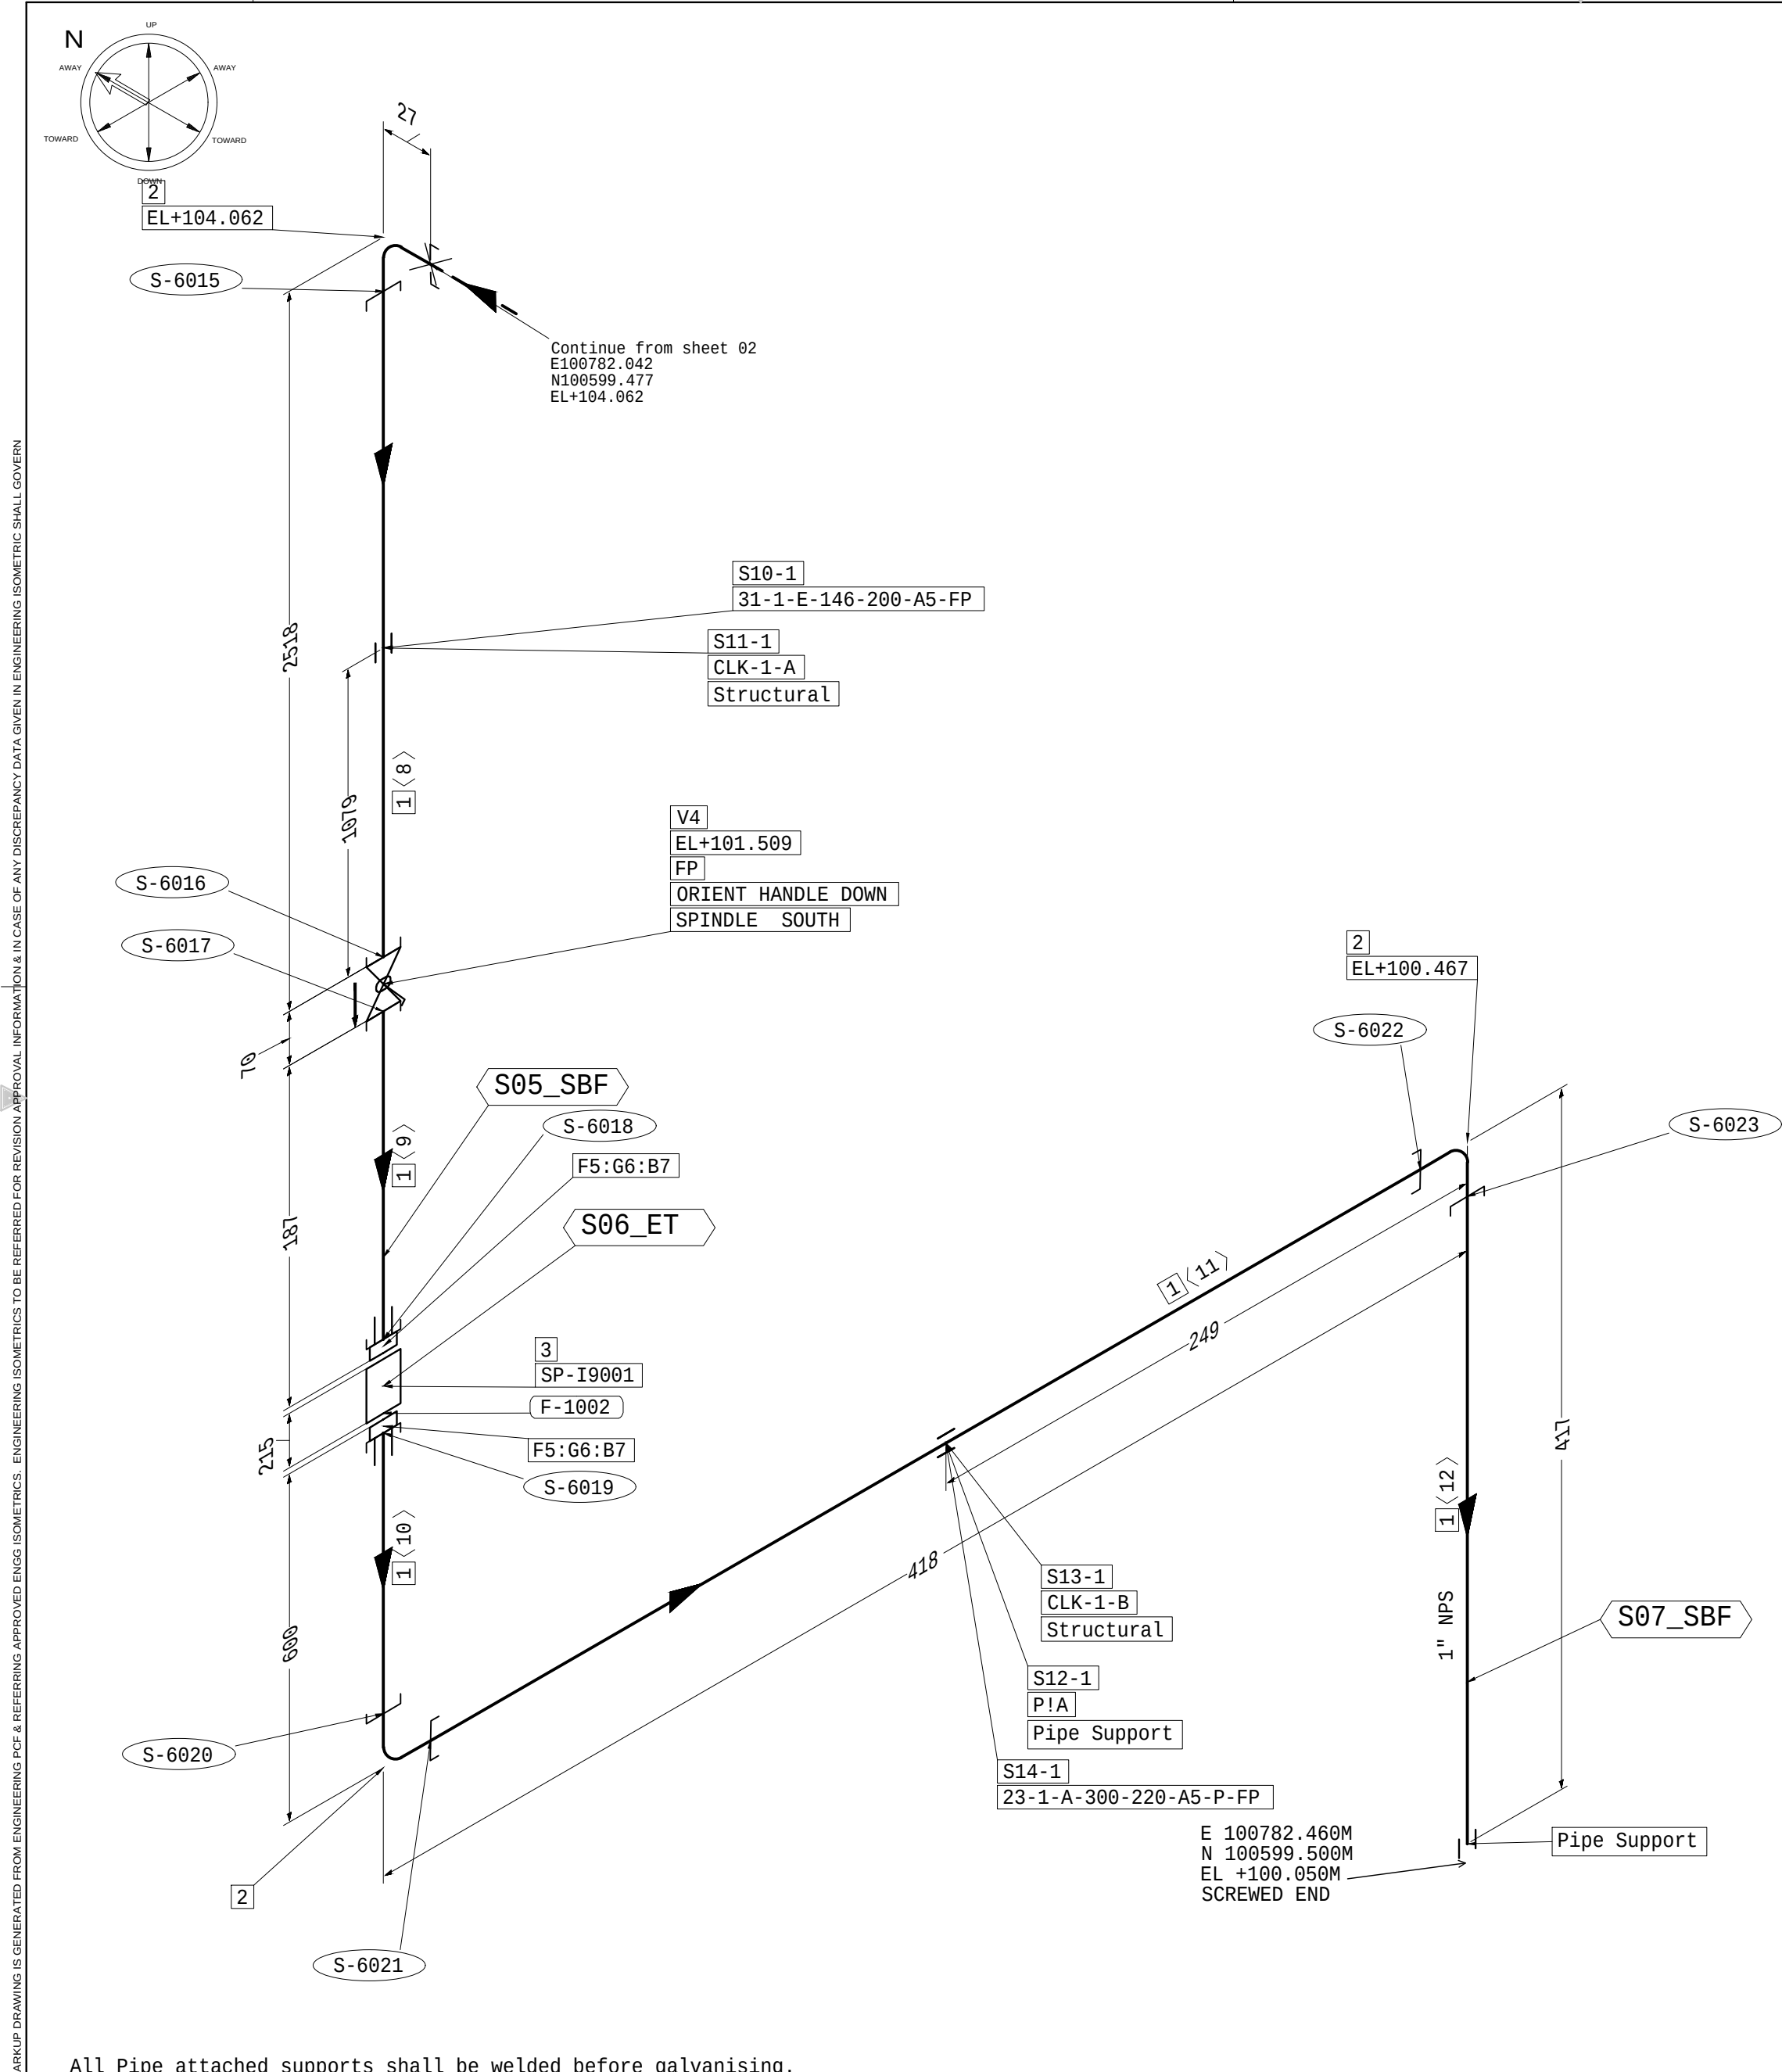

MATERIALS							STANDARD DETAIL REFERENCE DRAWINGS	
PT No.	DESCRIPTION			NPD(IN)	ITEM CODE	QTY	DETAILS HEAVY WELDING BOSSSES FOR THREADED CONNECTIONS CONSTRUCTION DETAILS AND DETAILS FOR ISOMETRIC PIPING INSULATION DETAILS FOR HOT PIPING INSULATION DETAILS FOR COLD PIPING INSTALLATION OF JACK SCREWS FOR FLANGED JOINTS	
PIPES							AE-036175 AD-036077 AA-036911 AA-036913 AC-036630	
1	PIPE SMLS 1" A106-B GALV STD NPT (M) B36.10M			1	PPS2AEAE01ZZABUUA	4.004	NOTES 1. MATERIAL SHOWN WITH A BROKEN LINE AND SPOOLS LISTED IN THE SAUDI ARAMCO FABRICATION LIST ARE NOT TO BE FURNISHED BY THE VENDOR. 2. PIPING DETAILS SHALL BE CUT AT ALL POINTS MARKED F.W. (FIELD WELD). 3. EACH FABRICATED SECTION SHALL BE CLEARLY MARKED WITH ITS CODE NUMBER. 4. UNLESS OTHERWISE NOTED: (A) ALL DIMENSIONS ARE TO FACE OF FLANGES. (B) BOLT HOLES ON FLANGES STRADDLE C. (C) WELDING ELBOWS ARE LONG RADIUS. 5. FABRICATION SHALL BE IN ACCORDANCE WITH SAUDI ARAMCO SPECIFICATION 01-SAMSS-10. 6. GASKET ALLOWANCE 7. PIPING MATERIAL IS <table><tr><th>PIPE SIZE</th><th>SCHEDULE</th><th>SPECIFICATION</th></tr><tr><td> </td><td> </td><td> </td></tr><tr><td> </td><td> </td><td> </td></tr><tr><td> </td><td> </td><td> </td></tr><tr><td> </td><td> </td><td> </td></tr></table> 8. WELDING STRESS RELIEF - YES ☐ NO ☐ 100% X-RAY ☐ SPOT X-RAY 01-SAMSS-10 ☐ 9. TESTING SHOP HYDROSTATIC TEST - YES ☐ NO ☐ THE SHOP HYDROSTATIC TEST SHALL BE CARRIED OUT ON PIECES HAVING ALL ENDS FLANGED. HYDROSTATIC TEST PRESSURE 10. ALL PIPING MATERIAL IS IN ACCORDANCE WITH SAUDI ARAMCO ENGINEERING SPECIFICATION SAESL-105 CLASS. ALL EXCEPTIONS ARE NOTED ON THE ISOMETRIC. 11. INSULATION REQUIRED - YES ☐ NO ☐ INSULATION SHOWN ON DRAWING							PIPE SIZE	SCHEDULE	SPECIFICATION	
PIPE SIZE	SCHEDULE	SPECIFICATION	
2	ELB 90° FRG LR 1" A105N GALV 3000# NPT (F) B16.11			1	PE72ADAE01ZZAA0ATA	3	
3	Piping Speciality Air Trap			1	SP-I9001	1	
VALVE	
4	TAG NO V0B-29-0I-AS-AF-AA-BFI BALL VAL FB MSS-SP-110 1" B61/B62 BRONZE TRIM WITH RTFE SEAT 2/3 PIECE CONST,FLT TYP NPTF 150# LEVER OPT			1	V0B290I01ASAFABFI	1	
FLANGES	
5	FLG SCRD RF 1" A105N GALV 150# 125 B16.5			1	PFH2ADAE01ZZAAAADH	2	
GASKET	
6	GSK SPR WND W/CS CENTERING RING + I - SS 1" 4.50 MM THICK SS316L+GRPH FILL 150# B16.20			1	PGUUB5AG01AIAAAZZC	2	
FASTSNERS	
7	BOLT, STUD+2 NUTS A193 B7/ A194 2H, CERAMIC FLP COAT B18.2.1/18.2.2 - 80 mm Length			0.5	PH8AB5AGAE00080ZZF	8	
SUPPORTS	
10	PIPE SUPPORT			1	31-1-E-146-200-A5-FP	1	
11	PIPE SUPPORT			1	CLK-1-A	1	
12	PIPE SUPPORT			1	P!A	1	
13	PIPE SUPPORT			1	CLK-1-B	1	
14	PIPE SUPPORT			1	23-1-A-300-220-A5-P-FP	1	
SPOOLS TO BE FABRICATED BY VENDOR	
<table><tr><th>NO. PIECES</th><th>MARK NO.</th><th>SIZE</th><th>WEIGHT LBS</th><th>NO. PIECES</th><th>MARK NO.</th><th>SIZE</th><th>WEIGHT LBS</th></tr><tr><td> </td><td> </td><td> </td><td> </td><td> </td><td> </td><td> </td><td> </td></tr><tr><td> </td><td> </td><td> </td><td> </td><td> </td><td> </td><td> </td><td> </td></tr><tr><td> 