


THIS SHEET MARKUP DRAWING IS GENERATED FROM ENGINEERING PDF & REFERRING APPROVED ENGG ISOMETRICS. ENGINEERING ISOMETRICS TO BE REFERRED FOR REVISION APPROVAL INFORMATION & IN CASE OF ANY DISCREPANCY DATA GIVEN IN ENGINEERING ISOMETRIC SHALL GOVERN

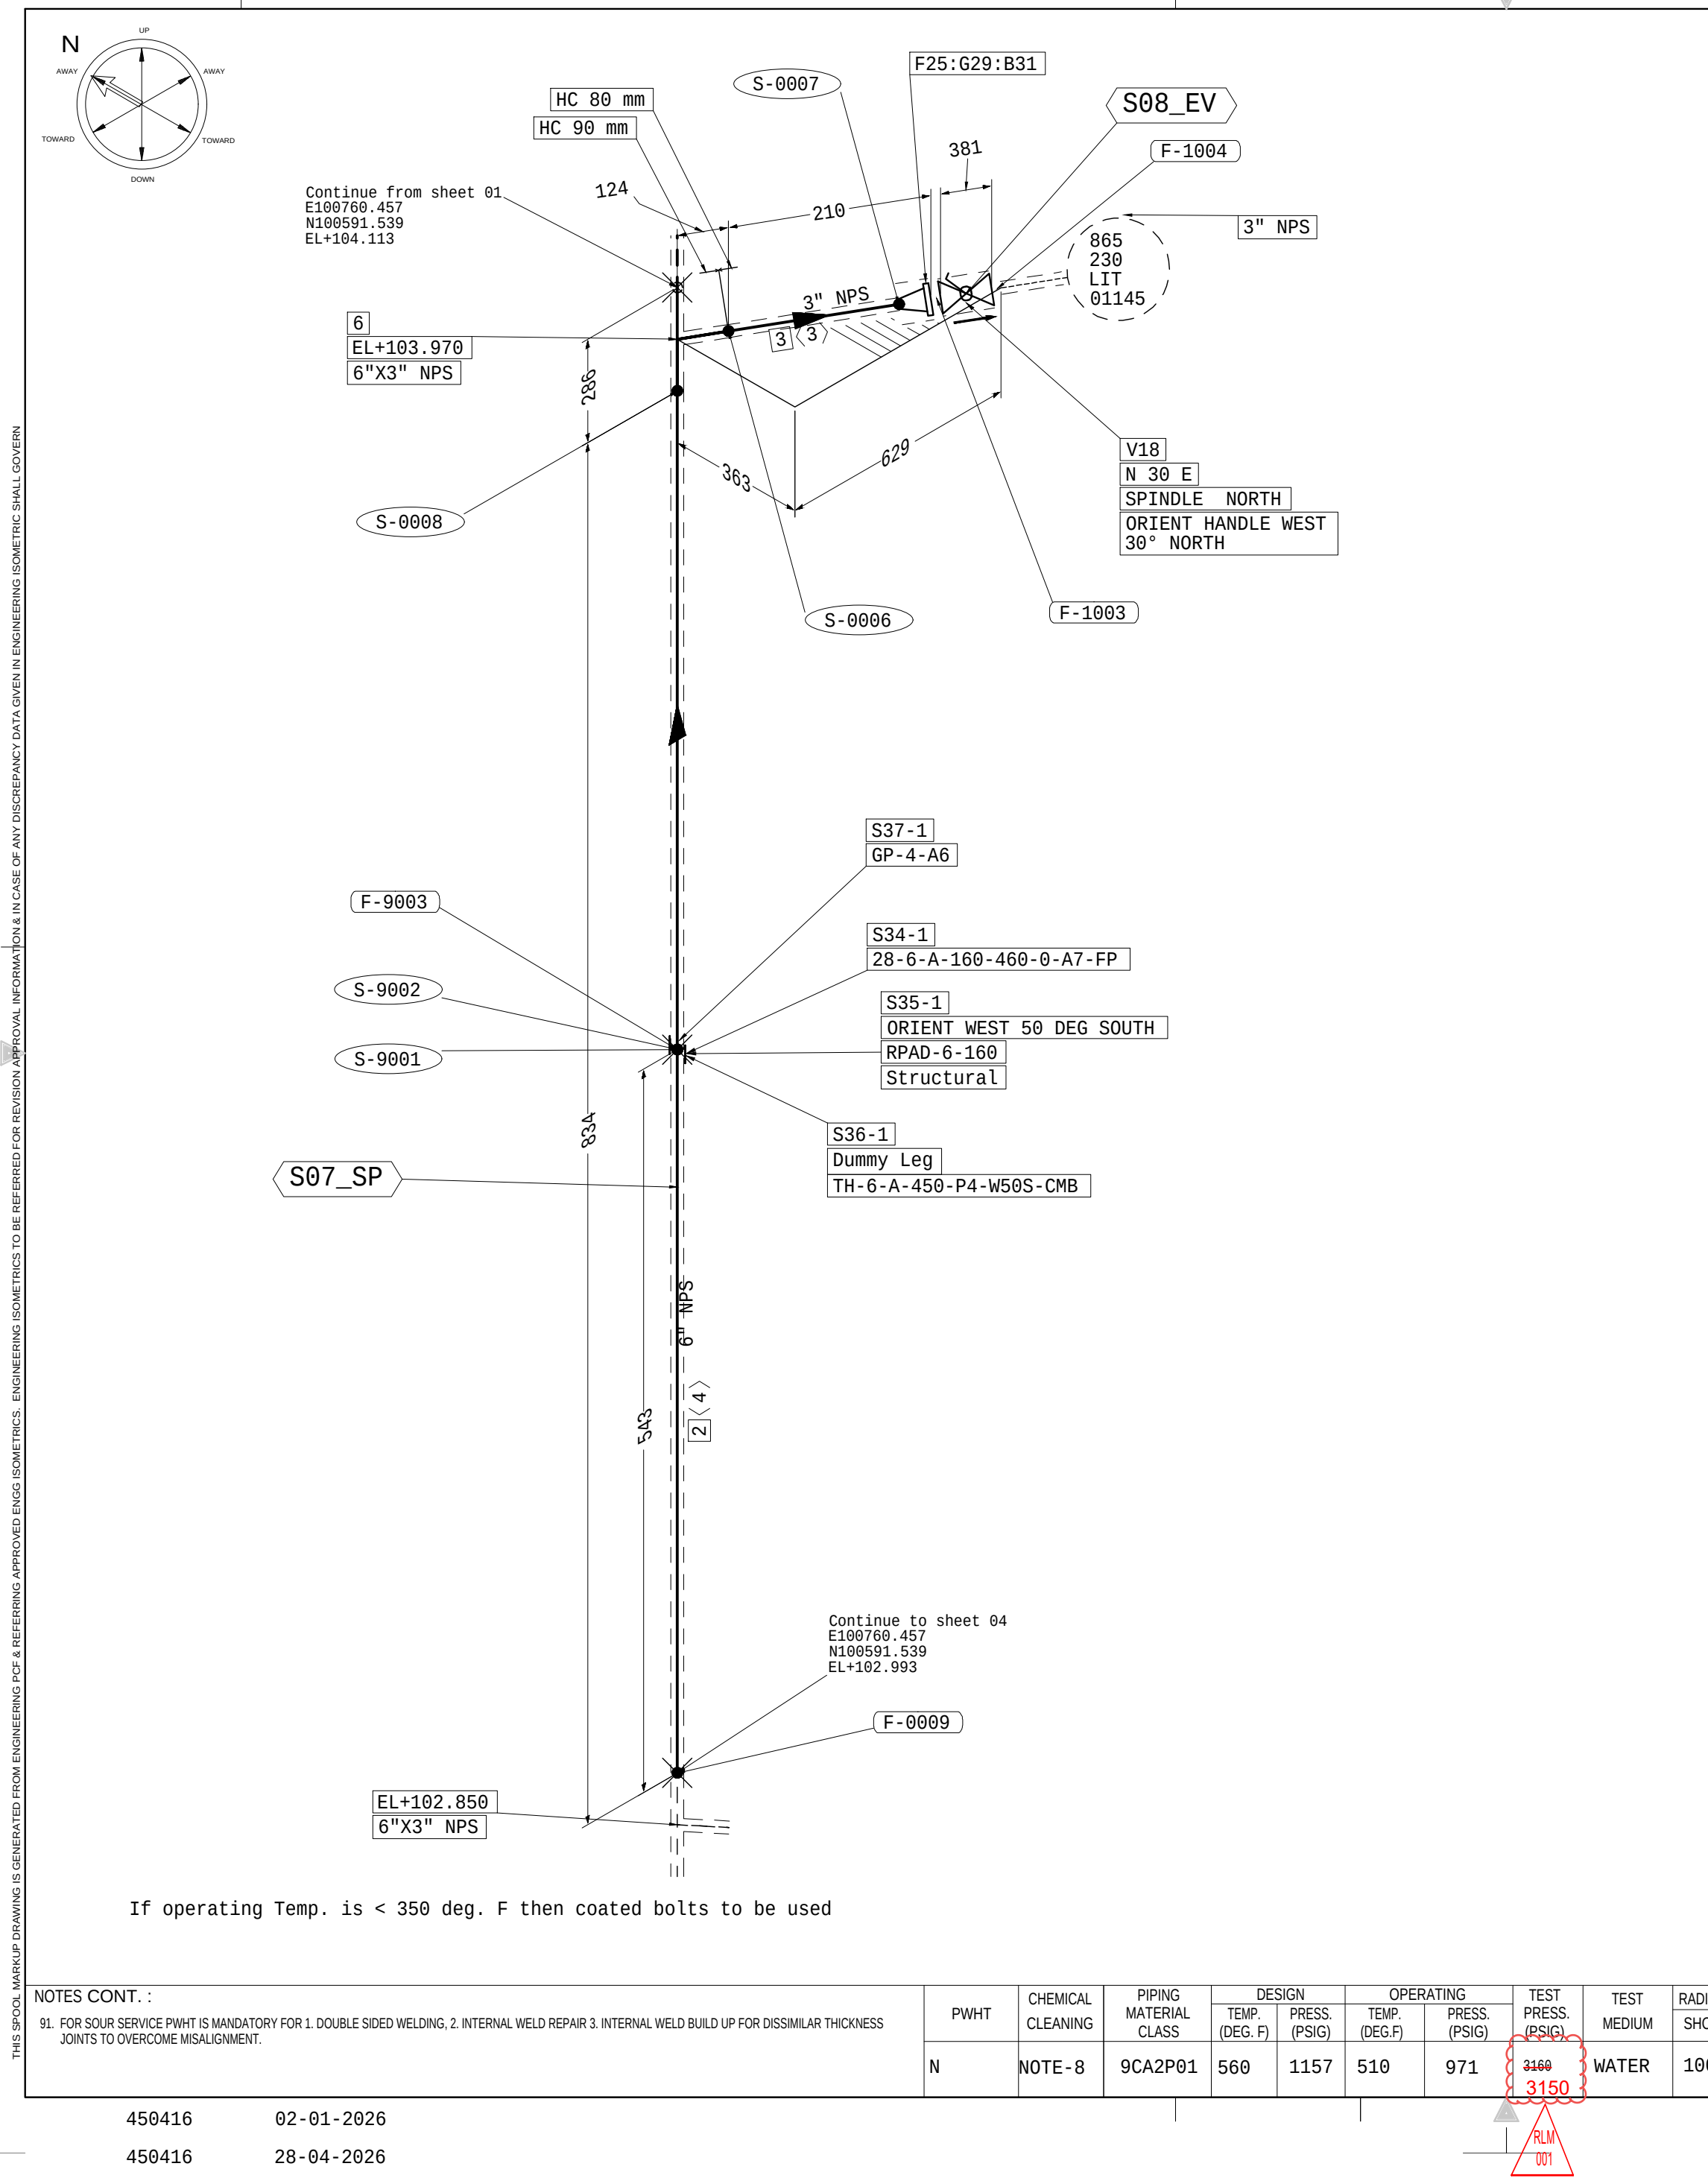

If operating Temp. is < 350 deg. F then coated bolts to be used

NOTES CONT. :

91. FOR SOUR SERVICE PWHT IS MANDATORY FOR 1. DOUBLE SIDED WELDING, 2. INTERNAL WELD REPAIR 3. INTERNAL WELD BUILD UP FOR DISSIMILAR THICKNESS JOINTS TO OVERCOME MISALIGNMENT.

PWHT	CHEMICAL CLEANING	PIPING MATERIAL CLASS	DESIGN		OPERATING		TEST PRESS. (PSIG)	TEST MEDIUM	RADIOGRAPHY %		INSULATION		TRACING	PAINTING	STRESS SYS NO.	LINE ID
			TEMP. (DEG. F)	PRESS. (PSIG)	TEMP. (DEG.F)	PRESS. (PSIG)			SHOP	FIELD	THK. (MM)	TYPE				
N	NOTE-8	9CA2P01	560	1157	510	971	3160 3150	WATER	100	100	90	HC	NA	APCS-11C		VT-D2314AN9-230A

MATERIALS						STANDARD DETAIL REFERENCE DRAWINGS	
PT No.	DESCRIPTION			NPD(IN)	ITEM CODE	QTY	DETAILS: HEAVY WELDING ROSSSES FOR THREADED CONNECTIONS CONSTRUCTION DETAILS AND DETAILS FOR ISOMETRIC PIPING INSULATION DETAILS FOR HOT PIPING INSULATION DETAILS FOR COLD PIPING INSTALLATION OF JACK SCREWS FOR FLANGED JOINTS	
PIPES							AE-036175 AD-036177 AA-036181 AA-036183 AC-036180	
2	PIPE SMLS 6" A333-6 XS BE B36.10M			6	PPSSA4AG06ZZABVAIA	0.834	NOTES	
3	PIPE SMLS 3" A333-6 S160 BE B36.10M			3	PPSSA4AG03ZZABTAIA	0.100	
FITTINGS							1. MATERIAL SHOWN WITH A BROKEN LINE AND SPOOLS LISTED IN THE SAUDI ARAMCO FABRICATION LIST ARE NOT TO BE FURNISHED BY THE VENDOR.	
6	TEE RED. SMLS 6" X 3" A420 WPL6 XS x S160 BE B16.9			6X3	PTS5AEAG0603AISAIQ	1	2. PIPING DETAILS SHALL BE CUT AT ALL POINTS MARKED F.W. (FIELD WELD).	
VALVE							3. EACH FABRICATED SECTION SHALL BE CLEARLY MARKED WITH ITS CODE NUMBER.	
18	TAG NO V11-DS-D4-AJ-AC-AF-KQY BALL VAL RB API 6D 3" A352-LCB SS 316 HF (BALL AND SEAT) SS316 STEM 2/3 PIECE CONST, TRUN MNT, FIRE SAFE RTJ 900# LOW TEMP SER, LNG PATN + CSO/CSC, LEVER OPT			3	V11DS403AJACAFKQY	1	4. UNLESS OTHERWISE NOTED: (A) ALL DIMENSIONS ARE TO FACE OF FLANGES. (B) BOLT HOLES ON FLANGES STRADDLE C. (C) WELDING ELBOWS ARE LONG RADIUS.	
FLANGES							5. FABRICATION SHALL BE IN ACCORDANCE WITH SAUDI ARAMCO SPECIFICATION 01-SAMSS-10.	
25	FLG WNRJT 3" A350LF2CL1 S160, 900# 32 B16.5			3	PFZ3F9AG03ZZAFCAH	1	6. GASKET ALLOWANCE	
29	GSK OCTG RTJ 3" SOFT IRON CL900 TYPE-R B16.20			3	PGNUAWAG03ASDQUA1C	1	7. PIPING MATERIAL IS	
FASTSNERS							<table><tr><th>PIPE SIZE</th><th>SCHEDULE</th><th>SPECIFICATION</th></tr><tr><td> </td><td> </td><td> </td></tr><tr><td> </td><td> </td><td> </td></tr><tr><td> </td><td> </td><td> </td></tr><tr><td> </td><td> </td><td> </td></tr><tr><td> </td><td> </td><td> </td></tr><tr><td> </td><td> </td><td> </td></tr></table>						PIPE SIZE	SCHEDULE	SPECIFICATION	
PIPE SIZE	SCHEDULE	SPECIFICATION	
31	BOLT, STUD+2 NUTS A320-L7/ A194-7 B18.2.1/18.2.2 - 160 mm Length			0.875	PH8ZMPAGAH00160ZZF	8	8. WELDING STRESS RELIEF - YES ☐ NO ☐ 100% X-RAY ☐ SPOT X-RAY 01-SAMSS-10 ☐	
SUPPORTS							9. TESTING SHOP HYDROSTATIC TEST - YES ☐ NO ☐ THE SHOP HYDROSTATIC TEST SHALL BE CARRIED OUT ON PIECES HAVING ALL ENDS FLANGED. HYDROSTATIC TEST PRESSURE	
34	PIPE SUPPORT			6	28-6-A-160-460-0-A7-FP	1	10. ALL PIPING MATERIAL IS IN ACCORDANCE WITH SAUDI ARAMCO ENGINEERING SPECIFICATION SAES-L-105 CLASS	
35	PIPE SUPPORT			6	RPAD-6-160	1	ALL EXCEPTIONS ARE NOTED ON THE ISOMETRIC.	
36	PIPE SUPPORT			6	TH-6-A-450-P4-W50S-CMB	1	11. INSULATION REQUIRED - YES ☐ NO ☐ INSULATION SHOWN ON DRAWING	
37	PIPE SUPPORT			6	GP-4-A6	1	
							SPOOLS TO BE FABRICATED BY VENDOR	
							<table><tr><th>NO. PIECES</th><th>MARK NO.</th><th>SIZE</th><th>WEIGHT LBS</th><th>NO. PIECES</th><th>MARK NO.</th><th>SIZE</th><th>WEIGHT LBS</th></tr><tr><td> </td><td> </td><td> </td><td> </td><td> </td><td> </td><td> </td><td> </td></tr><tr><td> </td><td> </td><td> </td><td> </td><td> </td><td> </td><td> </td><td> </td></tr><tr><td> 450416

02-01-2026

450416

28-04-2026

THIS DRAWING AND THE INFORMATION CONTAINED HEREIN ARE THE SOLE PROPERTY OF SAUDI ARAMCO. NO REPRODUCTION IN FULL OR IN PART, SHALL BE OBTAINED FROM THIS DRAWING WITHOUT THE WRITTEN CONSENT OF SAUDI ARAMCO.