


THIS SPOOL MARKUP DRAWING IS GENERATED FROM ENGINEERING PCF & REFERRING APPROVED ENGG ISOMETRICS. ENGINEERING ISOMETRICS TO BE REFERRED FOR REVISION APPROVAL INFORMATION & IN CASE OF ANY DISCREPANCY DATA GIVEN IN ENGINEERING ISOMETRIC SHALL GOVERN

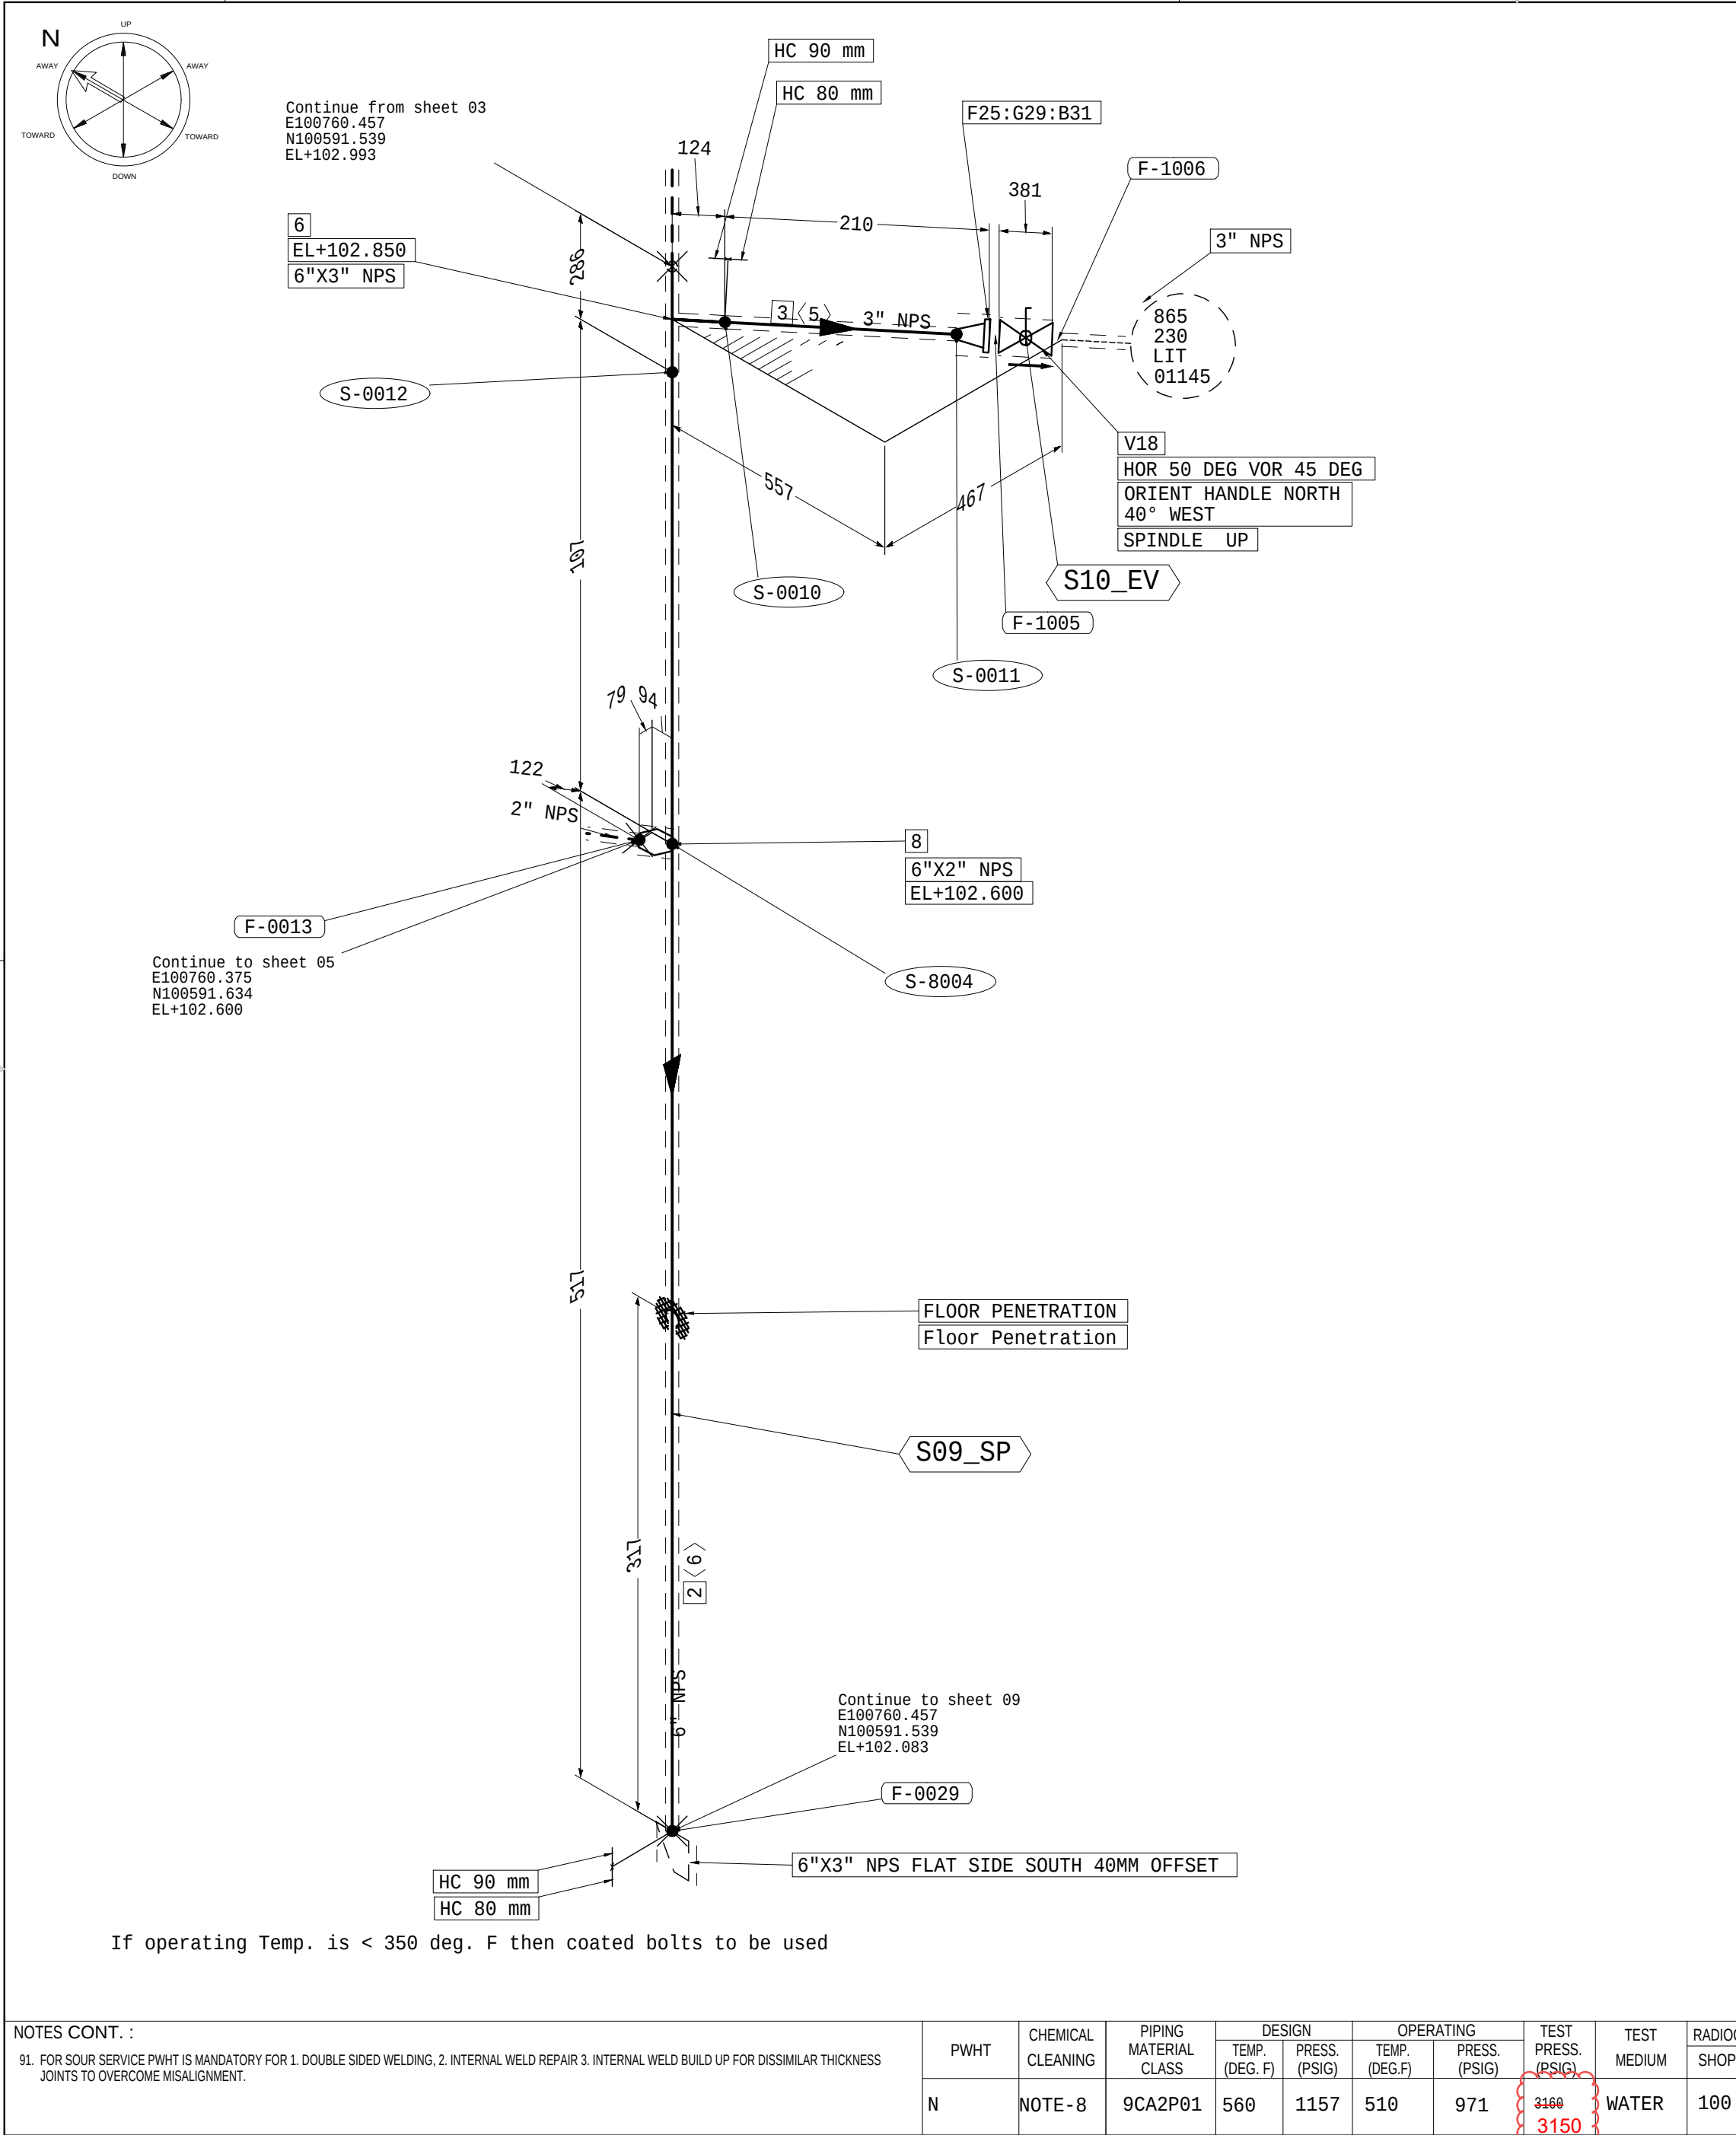

MATERIALS						STANDARD DETAIL REFERENCE DRAWINGS	
PT No.	DESCRIPTION			NPD(IN)	ITEM CODE	QTY	DETAILS HEAVY WELDING ROSSSES FOR THREADED CONNECTIONS CONSTRUCTION DETAILS AND DETAILS FOR ISOMETRIC PIPING INSULATION DETAILS FOR HOT PIPING INSULATION DETAILS FOR COLD PIPING INSTALLATION OF JACK SCREWS FOR FLANGED JOINTS	
PIPES							AE-036175 AD-036027 AA-036911 AA-036913 AC-036930	
2	PIPE SMLS 6" A333-6 XS BE B36.10M			6	PPSSA4AG06ZZABVAIA	0.624	NOTES	
3	PIPE SMLS 3" A333-6 S160 BE B36.10M			3	PPSSA4AG03ZZABTAIA	0.100	
FITTINGS							1. MATERIAL SHOWN WITH A BROKEN LINE AND SPOOLS LISTED IN THE SAUDI ARAMCO FABRICATION LIST ARE NOT TO BE FURNISHED BY THE VENDOR. 2. PIPING DETAILS SHALL BE CUT AT ALL POINTS MARKED F.W. (FIELD WELD). 3. EACH FABRICATED SECTION SHALL BE CLEARLY MARKED WITH ITS CODE NUMBER. 4. UNLESS OTHERWISE NOTED: (A) ALL DIMENSIONS ARE TO FACE OF FLANGES. (B) BOLT HOLES ON FLANGES STRADDLE C. (C) WELDING ELBOWS ARE LONG RADIUS. 5. FABRICATION SHALL BE IN ACCORDANCE WITH SAUDI ARAMCO SPECIFICATION 01-SAMSS-10. 6. GASKET ALLOWANCE 7. PIPING MATERIAL IS <table><tr><th>PIPE SIZE</th><th>SCHEDULE</th><th>SPECIFICATION</th></tr><tr><td> </td><td> </td><td> </td></tr><tr><td> </td><td> </td><td> </td></tr><tr><td> </td><td> </td><td> </td></tr><tr><td> </td><td> </td><td> </td></tr></table> 8. WELDING STRESS RELIEF - YES ☐ 100% X-RAY ☐ NO ☐ SPOT X-RAY (1-SAMES-10) ☐ 9. TESTING SHOP HYDROSTATIC TEST - YES ☐ THE SHOP HYDROSTATIC TEST SHALL BE CARRIED OUT ON PIECES HAVING ALL ENDS FLANGED. HYDROSTATIC TEST PRESSURE ☐ NO ☐ 10. ALL PIPING MATERIAL IS IN ACCORDANCE WITH SAUDI ARAMCO ENGINEERING SPECIFICATION SAES-1-105 CLASS ☐ ALL EXCEPTIONS ARE NOTED ON THE ISOMETRIC. 11. INSULATION REQUIRED - YES ☐ NO ☐ INSULATION SHOWN ON DRAWING ☐						PIPE SIZE	SCHEDULE	SPECIFICATION	
PIPE SIZE	SCHEDULE	SPECIFICATION	
6	TEE RED. SMLS 6" X 3" A420 WPL6 XS x S160 BE B16.9			6X3	PTS5AEAG0603AISAIQ	1	
8	WELT 6" X 2" A350LF2CL1 SOUR XS x S160 BE SP-97			6X2	PWL3F9RT0602AISAI7	1	
VALVE	
18	TAG NO V11-DS-D4-AJ-AC-AF-KQY BALL VAL RB API 6D 3" A352-LCB SS 316 HF (BALL AND SEAT), SS316 STEM 2/3 PIECE CONST, TRUN MNT, FIRE SAFE RTJ 900# LOW TEMP SER, LNG PATN + CSO/CSC, LEVER OPT			3	V11DS0403AJACAFKQY	1	
FLANGES	
25	FLG WNRTJ 3" A350LF2CL1 S160, 900# 32 B16.5			3	PFZ3F9AG03ZZAFCA BH	1	
GASKET	
29	GSK OCTG RTJ 3" SOFT IRON CL900 TYPE-R B16.20			3	PGNUAWAG03ASDQUA1C	1	
FASTSNERS	
31	BOLT, STUD+2 NUTS A320-L7/ A194-7 B18.2.1/18.2.2 - 160 mm Length			0.875	PH8ZMPAGAH00160ZZF	8	
SPOOLS TO BE FABRICATED BY VENDOR	
<table><tr><th>NO. PIECES</th><th>MARK NO.</th><th>SIZE</th><th>WEIGHT LBS</th><th>NO. PIECES</th><th>MARK NO.</th><th>SIZE</th><th>WEIGHT LBS</th></tr><tr><td> </td><td> </td><td> </td><td> </td><td> </td><td> </td><td> </td><td> </td></tr><tr><td> </td><td> </td><td> </td><td> </td><td> </td><td> </td><td> </td><td> </td></tr><tr><td> 