


THIS SPOOL MARKUP DRAWING IS GENERATED FROM ENGINEERING PDF & REFERRING APPROVED ENGG ISOMETRICS. ENGINEERING ISOMETRICS TO BE REFERRED FOR REVISION APPROVAL INFORMATION & IN CASE OF ANY DISCREPANCY DATA GIVEN IN ENGINEERING ISOMETRIC SHALL GOVERN

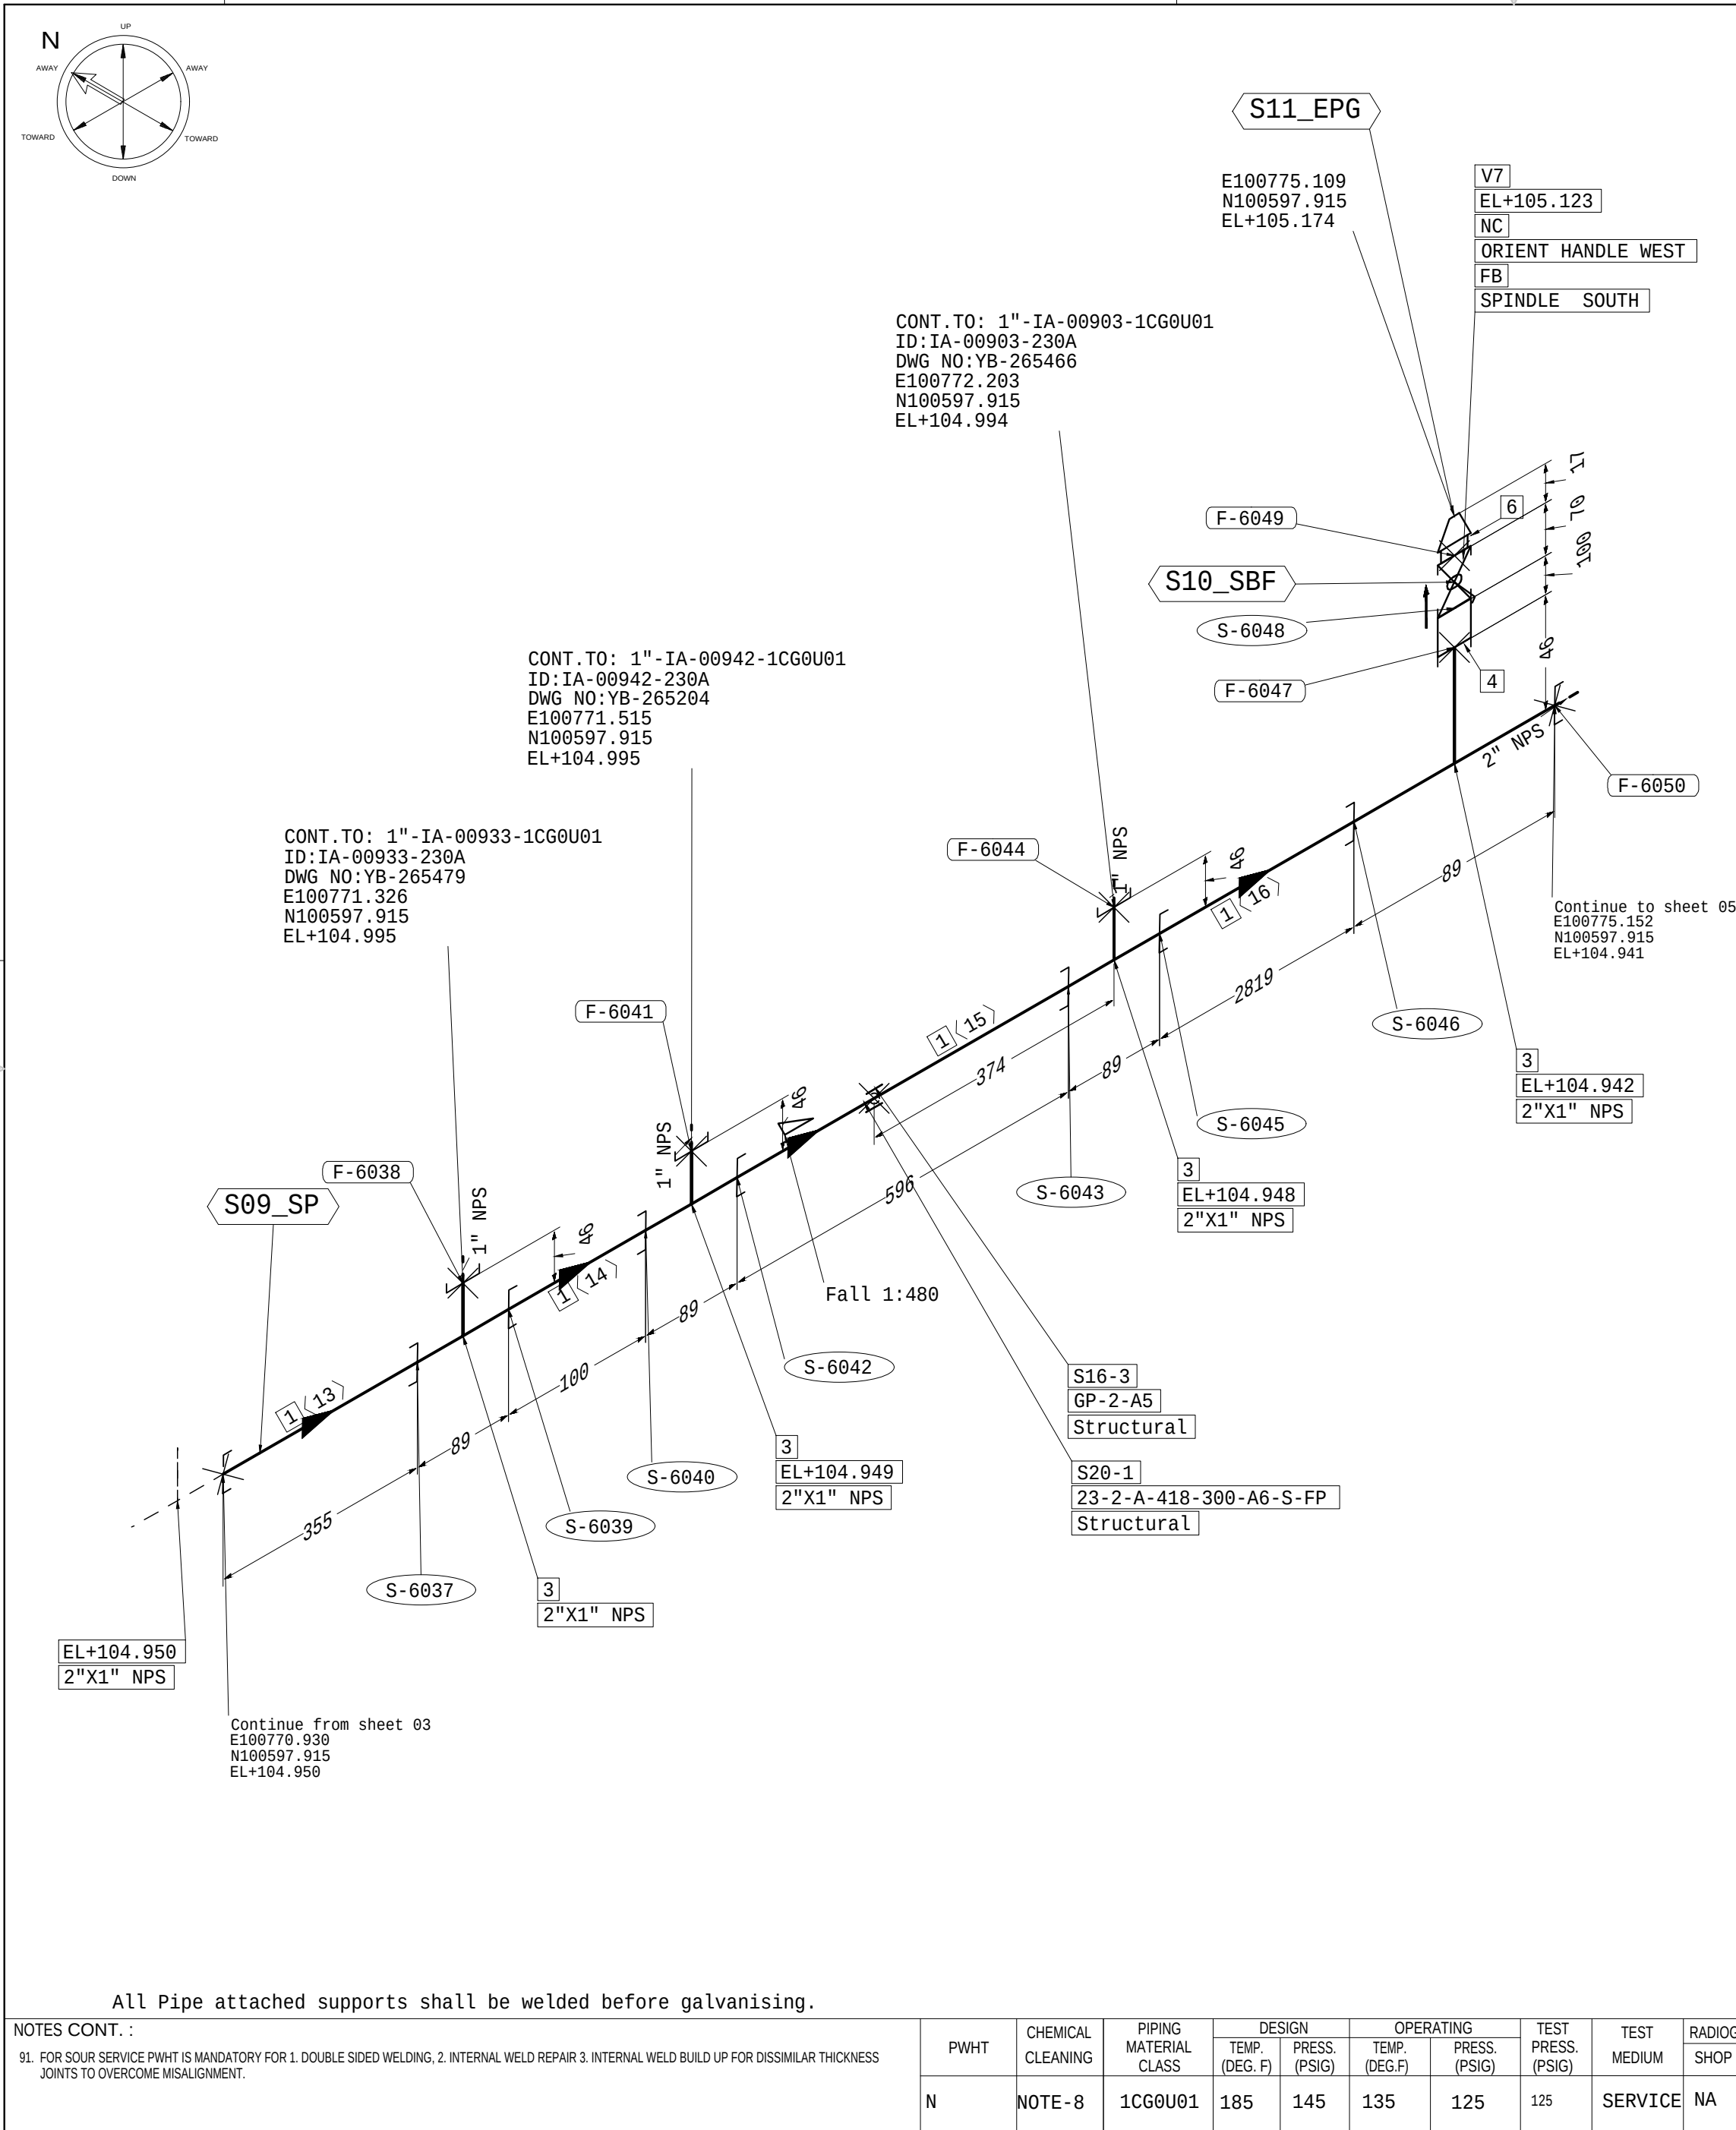

MATERIALS						STANDARD DETAIL REFERENCE DRAWINGS	
PT No.	DESCRIPTION			NPD(IN)	ITEM CODE	QTY	DETAILS OF HEAVY WELDING BOSSSES FOR THREADED CONNECTIONS CONSTRUCTION DETAILS AND DETAILS FOR ISOMETRIC PIPING INSULATION DETAILS FOR COLD PIPING INSTALLATION OF JACK SCREWS FOR FLANGED JOINTS	
	PIPES						NOTES 1. MATERIAL SHOWN WITH A BROKEN LINE AND SPOOLS LISTED IN THE SAUDI ARAMCO FABRICATION LIST ARE NOT TO BE FURNISHED BY THE VENDOR. 2. PIPING DETAILS SHALL BE CUT AT ALL POINTS MARKED F.W. (FIELD WELD). 3. EACH FABRICATED SECTION SHALL BE CLEARLY MARKED WITH ITS CODE NUMBER. 4. UNLESS OTHERWISE NOTED: (A) ALL DIMENSIONS ARE TO FACE OF FLANGES. (B) BOLT HOLES ON FLANGES STRADDLE C. (C) WELDING ELBOWS ARE LONG RADIUS. 5. FABRICATION SHALL BE IN ACCORDANCE WITH SAUDI ARAMCO SPECIFICATION 01-SAMSS-10. 6. GASKET ALLOWANCE 7. PIPING MATERIAL IS <table><thead><tr><th>PIPE SIZE</th><th>SCHEDULE</th><th>SPECIFICATION</th></tr></thead><tbody><tr><td></td><td></td><td></td></tr><tr><td></td><td></td><td></td></tr><tr><td></td><td></td><td></td></tr><tr><td></td><td></td><td></td></tr><tr><td></td><td></td><td></td></tr></tbody></table> 8. WELDING STRESS RELIEF - YES ☐ NO ☐ 100% X-RAY ☐ SPOT X-RAY 01-SAMSS-10 ☐ 9. TESTING SHOP HYDROSTATIC TEST - YES ☐ NO ☐ THE SHOP HYDROSTATIC TEST SHALL BE CARRIED OUT ON PIECES HAVING ALL ENDS FLANGED. HYDROSTATIC TEST PRESSURE 10. ALL PIPING MATERIAL IS IN ACCORDANCE WITH SAUDI ARAMCO ENGINEERING SPECIFICATION SAES-L-105 CLASS ALL EXCEPTIONS ARE NOTED ON THE ISOMETRIC. 11. INSULATION REQUIRED - YES ☐ NO ☐ INSULATION SHOWN ON DRAWING						PIPE SIZE	SCHEDULE	SPECIFICATION	
PIPE SIZE	SCHEDULE	SPECIFICATION	
1	PIPE SMLS 2" A106-B GALV STD NPT (M) B36.10M			2	PPS2AEAE02ZZABUAUA	3.870	
3	FITTINGS TEE RED. FRG 2" X 1" A105N GALV 3000# NPT (F) B16.11			2X1	PTR2ADAE0201AA0ATA	4	
4	PIPE NIPP SML TBE 1" X 100MM A106-B GALV XS NPT (M) B36.10M			1	PP52AEAE01AABVUAUA	1	
6	PLUG HEX HD 1" A105N GALV NPT (M) B16.11			1	PXC2ADAE01ZZZZZAUUA	1	
	VALVE	
7	TAG NO V0B-29-01-AS-AF-AA-BFI BALL VAL FB MSS-SP-110 1" B61/B62 BRONZE TRIM WITH RTFE SEAT 2/3 PIECE CONST, FLT TYP NPTF 150# LEVER OPT			1	V0B290101ASAFABFI	1	
16	PIPE SUPPORT			2	GP-2-A5	1	
20	PIPE SUPPORT			2	23-2-A-418-300-A6-S-FP	1	
SPOOLS TO BE FABRICATED BY VENDOR	
<table><thead><tr><th>NO. PIECES</th><th>MARK NO.</th><th>SIZE</th><th>WEIGHT LBS</th><th>NO. PIECES</th><th>MARK NO.</th><th>SIZE</th><th>WEIGHT LBS</th></tr></thead><tbody><tr><td></td><td></td><td></td><td></td><td></td><td></td><td></td><td></td></tr><tr><td></td><td></td><td></td><td></td><td></td><td></td><td></td><td></td></tr><tr><td></td><td></td><td></td><td></td><td></td><td></td><td></td><td></td></tr><tr><td></td><td></td><td></td><td></td><td></td><td></td><td></td><td></td></tr><tr><td></td><td></td><td></td><td></td><td></td><td></td><td></td><td></td></tr><tr><td></td><td></td><td></td><td></td><td></td><td></td><td></td><td></td></tr><tr><td></td><td></td><td></td><td></td><td></td><td></td><td></td><td></td></tr><tr><td></td><td></td><td></td><td></td><td></td><td></td><td></td><td></td></tr><tr><td></td><td></td><td></td><td></td><td></td><td></td><td></td><td></td></tr><tr><td></td><td></td><td></td><td></td><td></td><td></td><td></td><td></td></tr><tr><td></td><td></td><td></td><td></td><td></td><tdNO. PIECES	MARK NO.	SIZE	WEIGHT LBS	NO. PIECES	MARK NO.	SIZE	WEIGHT LBS	