


THIS SPOOL MARKUP DRAWING IS GENERATED FROM ENGINEERING PDF & REFERRING APPROVED ENGG ISOMETRICS. ENGINEERING ISOMETRICS TO BE REFERRED FOR REVISION APPROVAL INFORMATION & IN CASE OF ANY DISCREPANCY DATA GIVEN IN ENGINEERING ISOMETRIC SHALL GOVERN

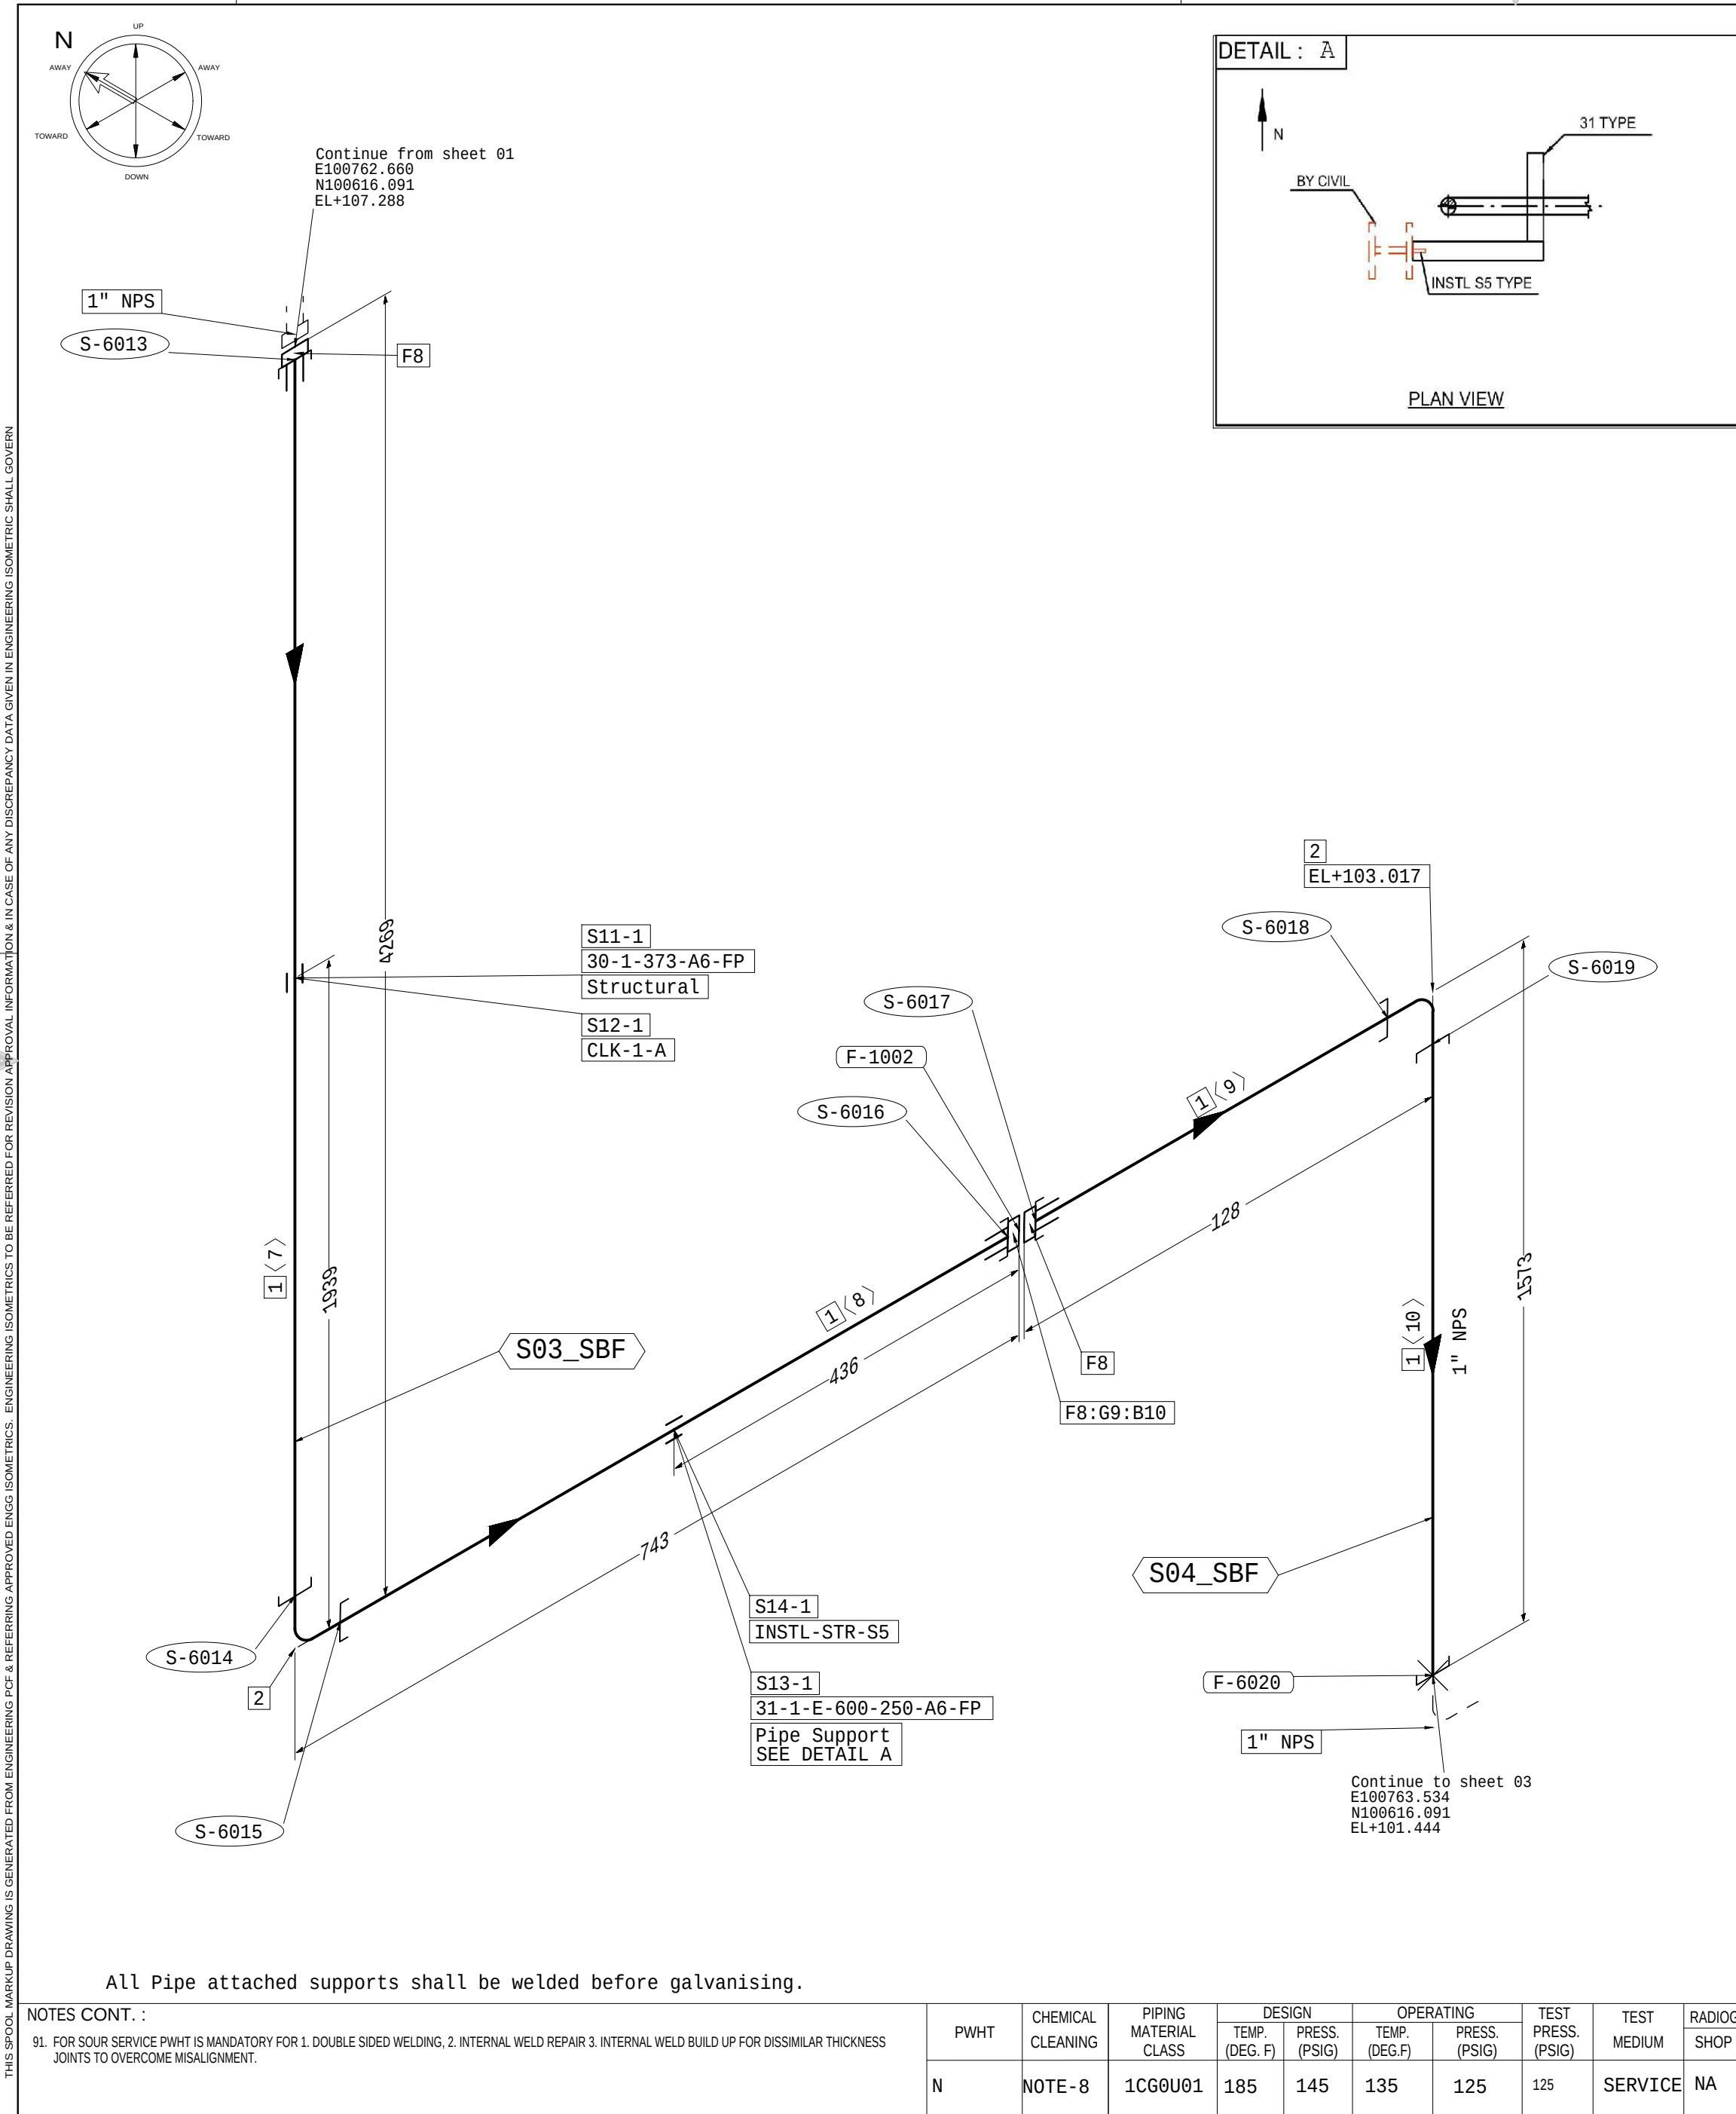

MATERIALS					STANDARD DETAIL REFERENCE DRAWINGS																			
PT No.	DESCRIPTION	NPD(IN)	ITEM CODE	QTY	DETAILS HEAVY WELDING BOSSSES FOR THREADED CONNECTIONS CONSTRUCTION DETAILS AND DETAILS FOR ISOMETRIC PIPING INSULATION DETAILS FOR HOT PIPING INSULATION DETAILS FOR COLD PIPING INSTALLATION OF JACK SCREWS FOR FLANGED JOINTS																			
PIPES					AE-036175 AD-036027 AA-036911 AA-036913 AC-036630																			
1	PIPE SMLS 1" A106-B GALV STD NPT (M) B36.10M	1	PPS2AEAE01ZZABUUA	6.605	NOTES 1. MATERIAL SHOWN WITH A BROKEN LINE AND SPOOLS LISTED IN THE SAUDI ARAMCO FABRICATION LIST ARE NOT TO BE FURNISHED BY THE VENDOR. 2. PIPING DETAILS SHALL BE CUT AT ALL POINTS MARKED F.W. (FIELD WELD). 3. EACH FABRICATED SECTION SHALL BE CLEARLY MARKED WITH ITS CODE NUMBER. 4. UNLESS OTHERWISE NOTED: (A) ALL DIMENSIONS ARE TO FACE OF FLANGES. (B) BOLT HOLES ON FLANGES STRADDLE C. (C) WELDING ELBOWS ARE LONG RADIUS. 5. FABRICATION SHALL BE IN ACCORDANCE WITH SAUDI ARAMCO SPECIFICATION 01-SAMSS-10. 6. GASKET ALLOWANCE 7. PIPING MATERIAL IS <table><tr><th>PIPE SIZE</th><th>SCHEDULE</th><th>SPECIFICATION</th></tr><tr><td> </td><td> </td><td> </td></tr><tr><td> </td><td> </td><td> </td></tr><tr><td> </td><td> </td><td> </td></tr><tr><td> </td><td> </td><td> </td></tr></table> 8. WELDING STRESS RELIEF - YES ☐ NO ☐ 100% X-RAY ☐ SPOT X-RAY 01-SAMSS-10 ☐ 9. TESTING SHOP HYDROSTATIC TEST - YES ☐ NO ☐ THE SHOP HYDROSTATIC TEST SHALL BE CARRIED OUT ON PIECES HAVING ALL ENDS FLANGED. HYDROSTATIC TEST PRESSURE 10. ALL PIPING MATERIAL IS IN ACCORDANCE WITH SAUDI ARAMCO ENGINEERING SPECIFICATION SAES-L-105 CLASS ALL EXCEPTIONS ARE NOTED ON THE ISOMETRIC. 11. INSULATION REQUIRED - YES ☐ NO ☐ INSULATION SHOWN ON DRAWING					PIPE SIZE	SCHEDULE	SPECIFICATION												
PIPE SIZE	SCHEDULE	SPECIFICATION																						
2	ELB 90° FRG LR 1" A105N GALV 3000# NPT (F) B16.11	1	PE72ADAE01ZZAA0ATA	2																				
8	FLG SCRD RF 1" A105N GALV 150# 125 B16.5	1	PFH2ADAE01ZZAAAADH	3																				
GASKET																								
9	GSK SPR WND W/CS CENTERING RING + I - SS 1" 4.50 MM THICK SS316L+GRPH FILL 150# B16.20	1	PGUUB5AG01AIAAAZZC	1																				
FASTSNERS																								
10	BOLT, STUD+2 NUTS A193 B7/ A194 2H, CERAMIC FLP COAT B18.2.1/18.2.2 - 80 mm Length	0.5	PH8AB5AGAE00080ZZF	4																				
SUPPORTS																								
11	PIPE SUPPORT	1	30-1-373-A6-FP	1																				
12	PIPE SUPPORT	1	CLK-1-A	1																				
13	PIPE SUPPORT	1	31-1-E-600-250-A6-FP	1																				
14	PIPE SUPPORT	1	INSTL-STR-S5	1																				

SPOOLS TO BE FABRICATED BY VENDOR							
NO. PIECES	MARK NO.	SIZE	WEIGHT LBS	NO. PIECES	MARK NO.	SIZE	WEIGHT LBS

SPOOLS TO BE FABRICATED BY SAUDI ARAMCO						
NO. PIECES	MARK NO.	SIZE	NO. PIECES	MARK NO.	SIZE	

REFERENCE DRAWINGS						
PIPING PLAN						
P&ID NO.			YA-221234-001			
PLOT PLAN KEY PLAN NO.			TA-293108			
INDEX FOR PIPING ISO (AG)			PP-865-LI-0003			
INDEX FOR PIPING ISO (UG)			PP-865-LI-0004			

450437 13-02-2026

450444 21-04-2026

THIS DRAWING AND THE INFORMATION CONTAINED HEREIN ARE THE SOLE PROPERTY OF SAUDI ARAMCO. NO REPRODUCTION IN FULL OR IN PART, SHALL BE OBTAINED FROM THIS DRAWING WITHOUT THE WRITTEN CONSENT OF SAUDI ARAMCO.