
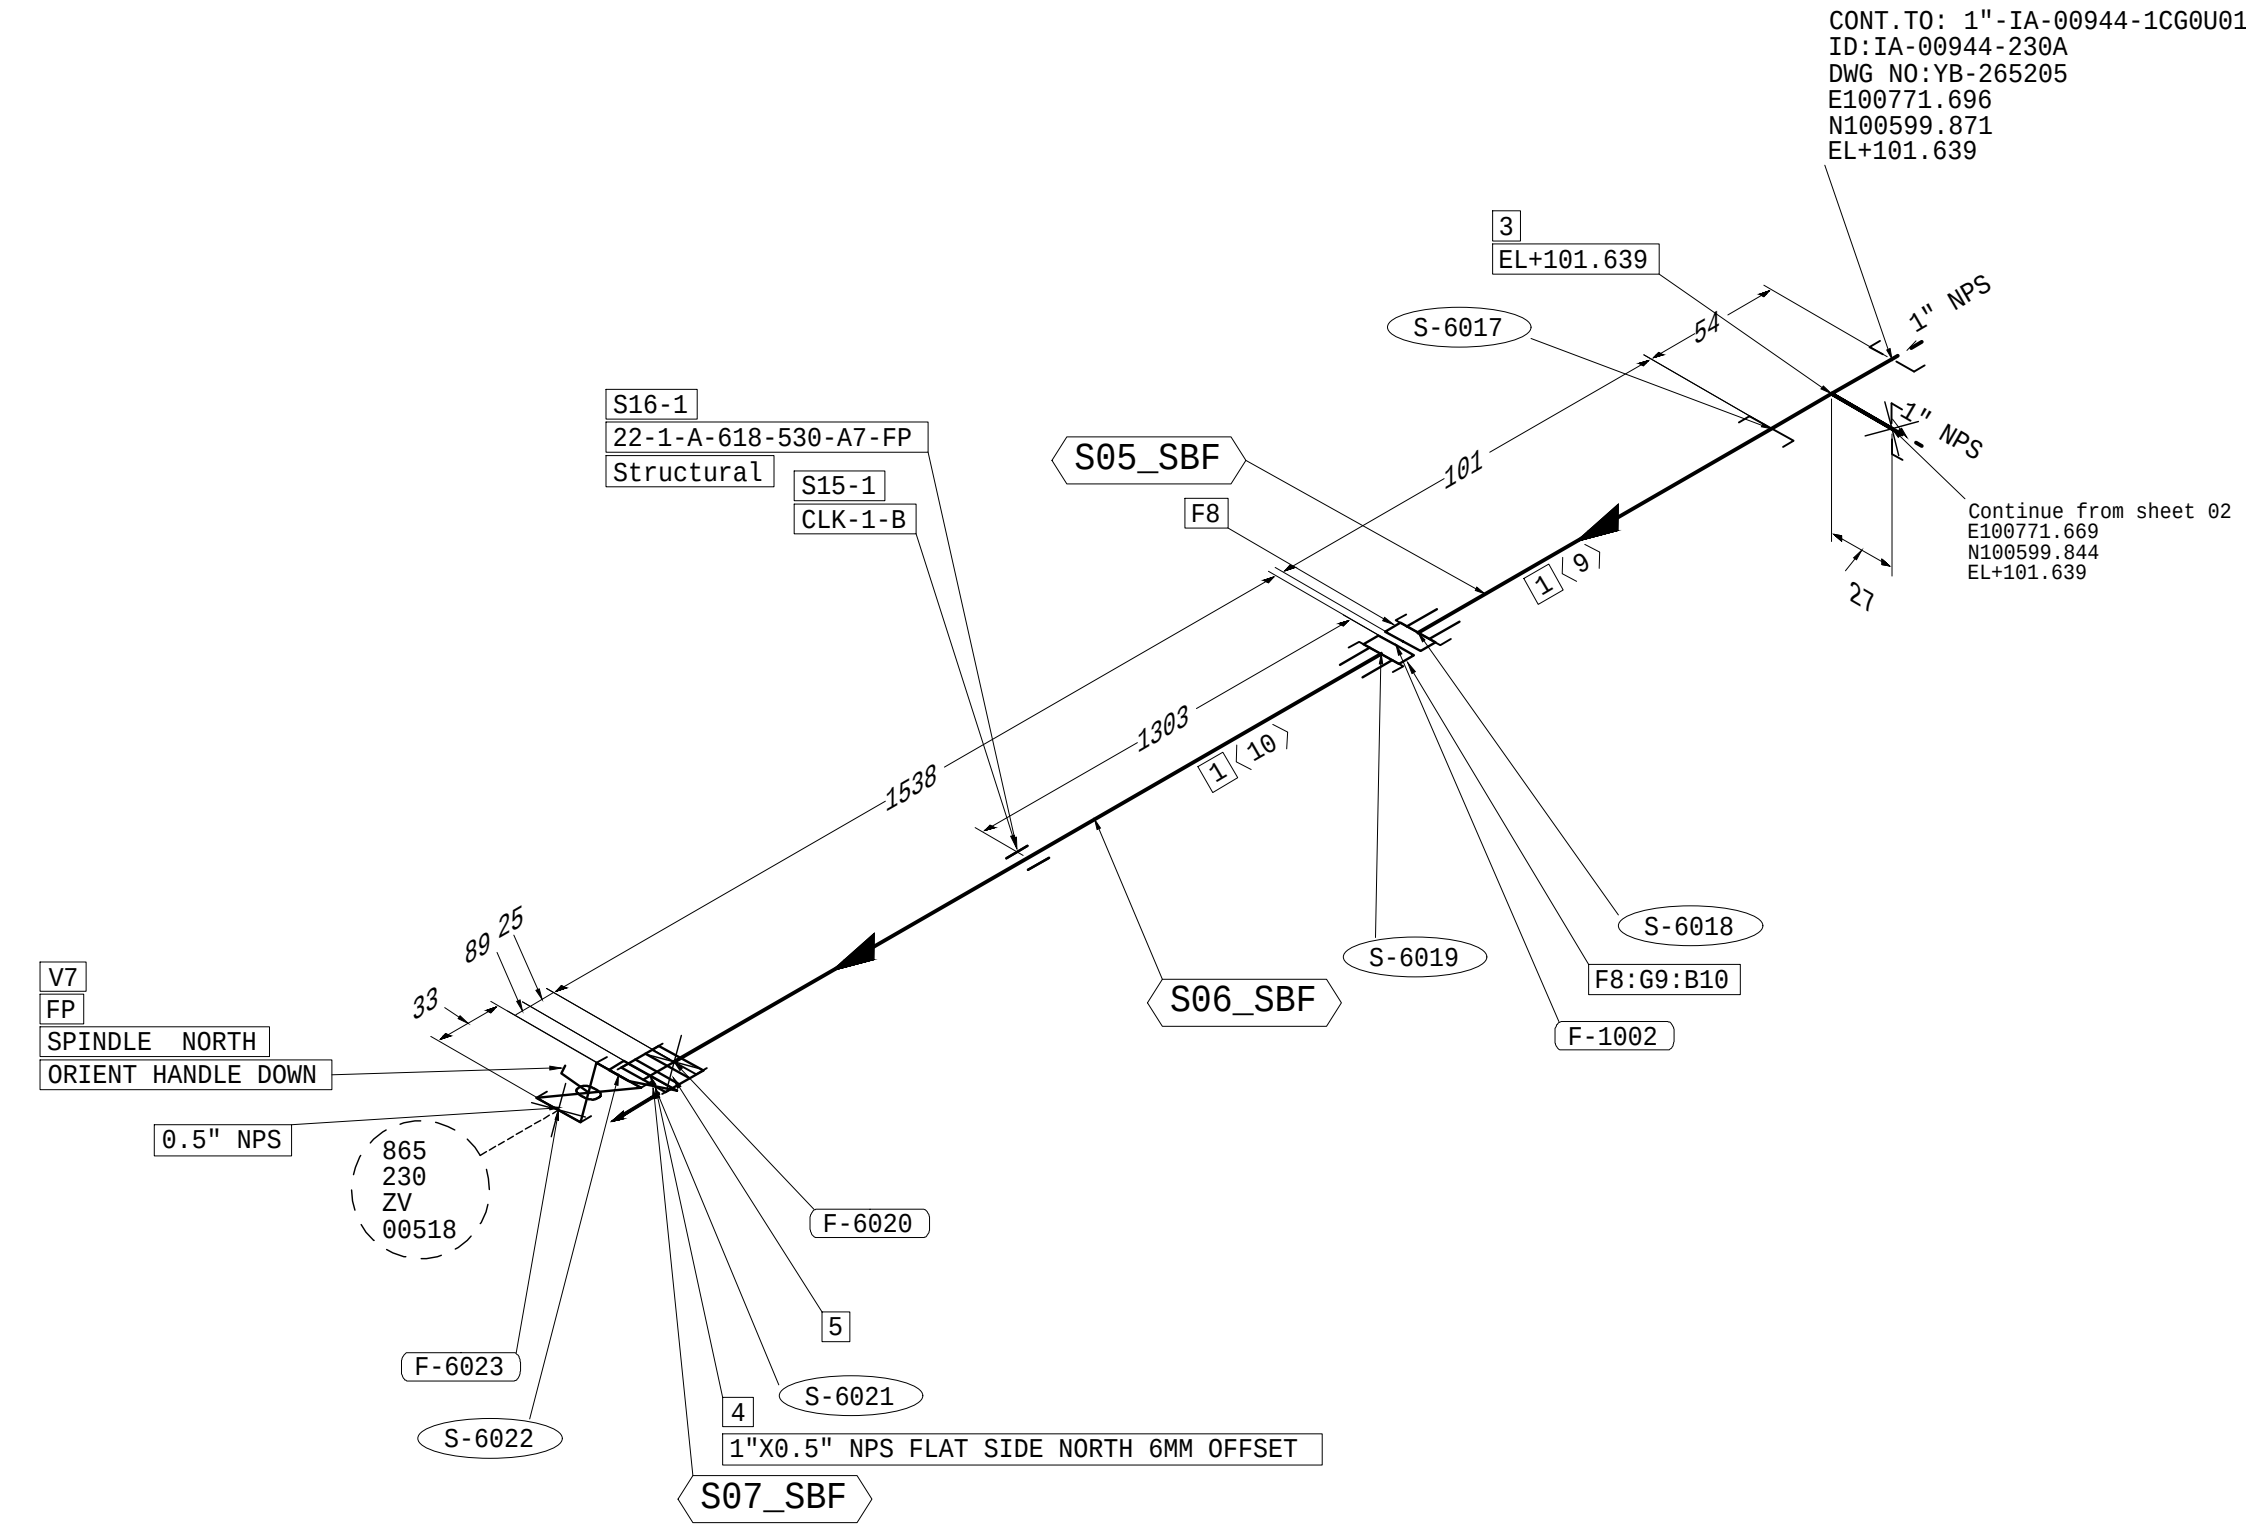


THIS SPOOL MARKUP DRAWING IS GENERATED FROM ENGINEERING PDF & REFERRING APPROVED ENGG ISOMETRICS. ENGINEERING ISOMETRICS TO BE REFERRED FOR REVISION APPROVAL INFORMATION & IN CASE OF ANY DISCREPANCY DATA GIVEN IN ENGINEERING ISOMETRIC SHALL GOVERN

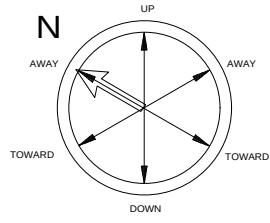

CONT. TO: 1"-IA-00944-1CG0U01
ID:IA-00944-230A
DWG NO:YB-265205
E100771.696
N100599.871
EL+101.639

Continue from sheet 02
E100771.669
N100599.844
EL+101.639

All Pipe attached supports shall be welded before galvanising.

MATERIALS										STANDARD DETAIL REFERENCE DRAWINGS									
PT No.	DESCRIPTION	NPD(IN)	ITEM CODE	QTY	DETAILS HEAVY WELDING BOLTS FOR THREADED CONNECTIONS CONSTRUCTION DETAILS AND DETAILS FOR ISOMETRIC PIPING INSULATION DETAILS FOR HOT PIPING INSULATION DETAILS FOR COLD PIPING INSTALLATION OF JACK SCREWS FOR FLANGED JOINTS														
PIPES																			
1	PIPE SMLS 1" A106-B GALV STD NPT (M) B36.10M	1	PPS2AEAE01ZZABUUA	1.640															
FITTINGS																			
3	TEE EQ. FRG 1" A105N GALV 3000# NPT (F) B16.11	1X1	PTE2ADAE01ZZAA0ATA	1															
4	SWG ECC 1" X 1/2" A234-WPB GALV STD NPT (M) SP-95	1X0.5	PR22AAE01AEABUUA9	1															
5	CPLG. FULL 1" A105N GALV 3000# NPT (F) B16.11	1	PX52ADAE01ZZAA0ATA	1															
VALVE																			
7	TAG NO V0B-29-01-AS-AF-AA-BFI BALL VAL FB MSS-SP-110 1/2" B61/B62 BRONZE TRIM WITH RTFE SEAT 2/3 PIECE CONST,FLT TYP NPTF 150# LEVER OPT	0.5	V0B290IAEASAFABFI	1															
FLANGES																			
8	FLG SCRD RF 1" A105N GALV 150# 125 B16.5	1	PFH2ADAE01ZZAAAADH	2															
GASKET																			
9	GSK SPR WND W/CS CENTERING RING + I - SS 1" 4.50 MM THICK SS316L+GRPH FILL 150# B16.20	1	PGUUB5AG01AIAAAZZC	1															
FASTSNERS																			
10	BOLT, STUD+2 NUTS A193 B7/ A194 2H, CERAMIC FLP COAT B18.2.1/18.2.2 - 80 mm Length	0.5	PH8AB5AGAE00080ZZF	4															
SUPPORTS																			
15	PIPE SUPPORT	1	CLK-1-B	1															
16	PIPE SUPPORT	1	22-1-A-618-530-A7-FP	1															

PIPE CUT LENGTH SUMMARY										ISO For									
SPL No.	NPD	PC No.	LENGTH	ALLOWANCE	TOTAL LENGTH	SXX_Spool Sequence Number (S01,02, SXX_SP - Fab. Spool SXX_PP - Fab. P to P Doubling (0-9M+0M) SXX_RP - Erec. Random Pipe (0M,12M) SXX_LP - Erec. Part Loose Fittings SXX_EP - Erec. Flange (F-Loose Flange, FFE-Bolt, FFS-Spectacle) SXX_EV - Erec. valve SXX_EPG - Erec. Pipe Plug SXX_SBF - Small Bore Spool Fab. SXX_SBE - Small Bore Spool Erec. SXX_SBD - Small Bore Spool Drain SXX_SBV - Small Bore Spool Vent													
S05_SBF	1	<9>	0.101	0.000	0.101	PART NUMBER													
S06_SBF	1	<10>	1.538	0.000	1.538	PIECE NUMBER													

NOTES :										BUTT WELD FIELD WELD									
1. ALL COORDINATES AND ELEVATIONS ARE IN 'METER' AND ALL DIMENSIONS ARE IN 'MM'. 2. PIPE QUANTITY IS IN METERS AND OTHER QUANTITY IN NUMBERS. 3. FOR STANDARD SUPPORT, REFER DOC. NO. "PP-866-ST-0001" 4. IN CASE OF ANY DISCREPANCY FOR LINE CONDITIONS, LINE DATA GIVEN IN LINE LIST SHALL GOVERN 5. FOR SMALL BORE LINES, DIMENSION & ROUTING SHALL BE FIELD ADJUSTED. 6. THE SPECIFIED THEORETICAL LOCATION OF EQUIPMENT NOZZLES, SUPPORTING STRUCTURE SHALL BE VERIFIED BEFORE INSTALLING THE PIPING & INTOLERABLE DISCREPANCIES SHALL BE DISCUSSED WITH DESIGN SITE ENGINEER. 7. ALL THREADED CONNECTION SHALL BE SEAL WELDED, EXCEPT DRAIN AND VENT PLUG. 8. REFER LINE LIST. 9. ALL PRESSURE WELDS, OTHER THAN BUTT WELDS, INCLUDING BRANCH CONNECTIONS SUCH AS BRANCH-OLETS, AND BOSS) SHALL BE 100% PTMT EXAMINED. ALL ATTACHMENT WELDS ON PRESSURIZED COMPONENTS THAT ARE NOT HYDROTESTED AFTER MAKING THE ATTACHMENT WELD SHALL BE 100% PTMT EXAMINED.										INSULATED PIPE TRACED PIPE PIPE SUPPORT PLATFORM PENETRATION SOCKET WELD SCREWED JOINT									

DESIGN CERTIFICATION (DESIGN AGENCY'S)										REVIEW FOR KEY DRAWINGS (SAUDI ARAMCO)										OTHER																													
ENGG./DATE										CERTIFIED BY/DATE										CONST. AGENCY/DATE										OPERATIONS/DATE										BY/DATE									
REV. NO.										DATE										REVISION DESCRIPTION																													

JOB ORDER/REV. NO.										THIS REVISION IS NOT TO BE USED FOR CONSTRUCTION UNLESS CERTIFIED AND DATED														
10-14815-0003																								
SAUDI ARABIAN OIL COMPANY																								
ISOM 1" -IA-00942-1CG0U01																								
IA SERVICE																								
JFGP GAS PROCESSING TRAIN-2																								
JAFURAH										SAUDI ARABIA														
PLANT NO.					INDEX					DRAWING NUMBER					SHT. NO.					REV. NO.				
865					L					YB-265204					030f03					00-00				

SITE REV. NO.										RESTRICTED										SMART										CADD-03									
001																																							

450437 13-02-2026

450444 21-04-2026

THIS DRAWING AND THE INFORMATION CONTAINED HEREIN ARE THE SOLE PROPERTY OF SAUDI ARAMCO. NO REPRODUCTION IN FULL OR IN PART, SHALL BE OBTAINED FROM THIS DRAWING WITHOUT THE WRITTEN CONSENT OF SAUDI ARAMCO.