
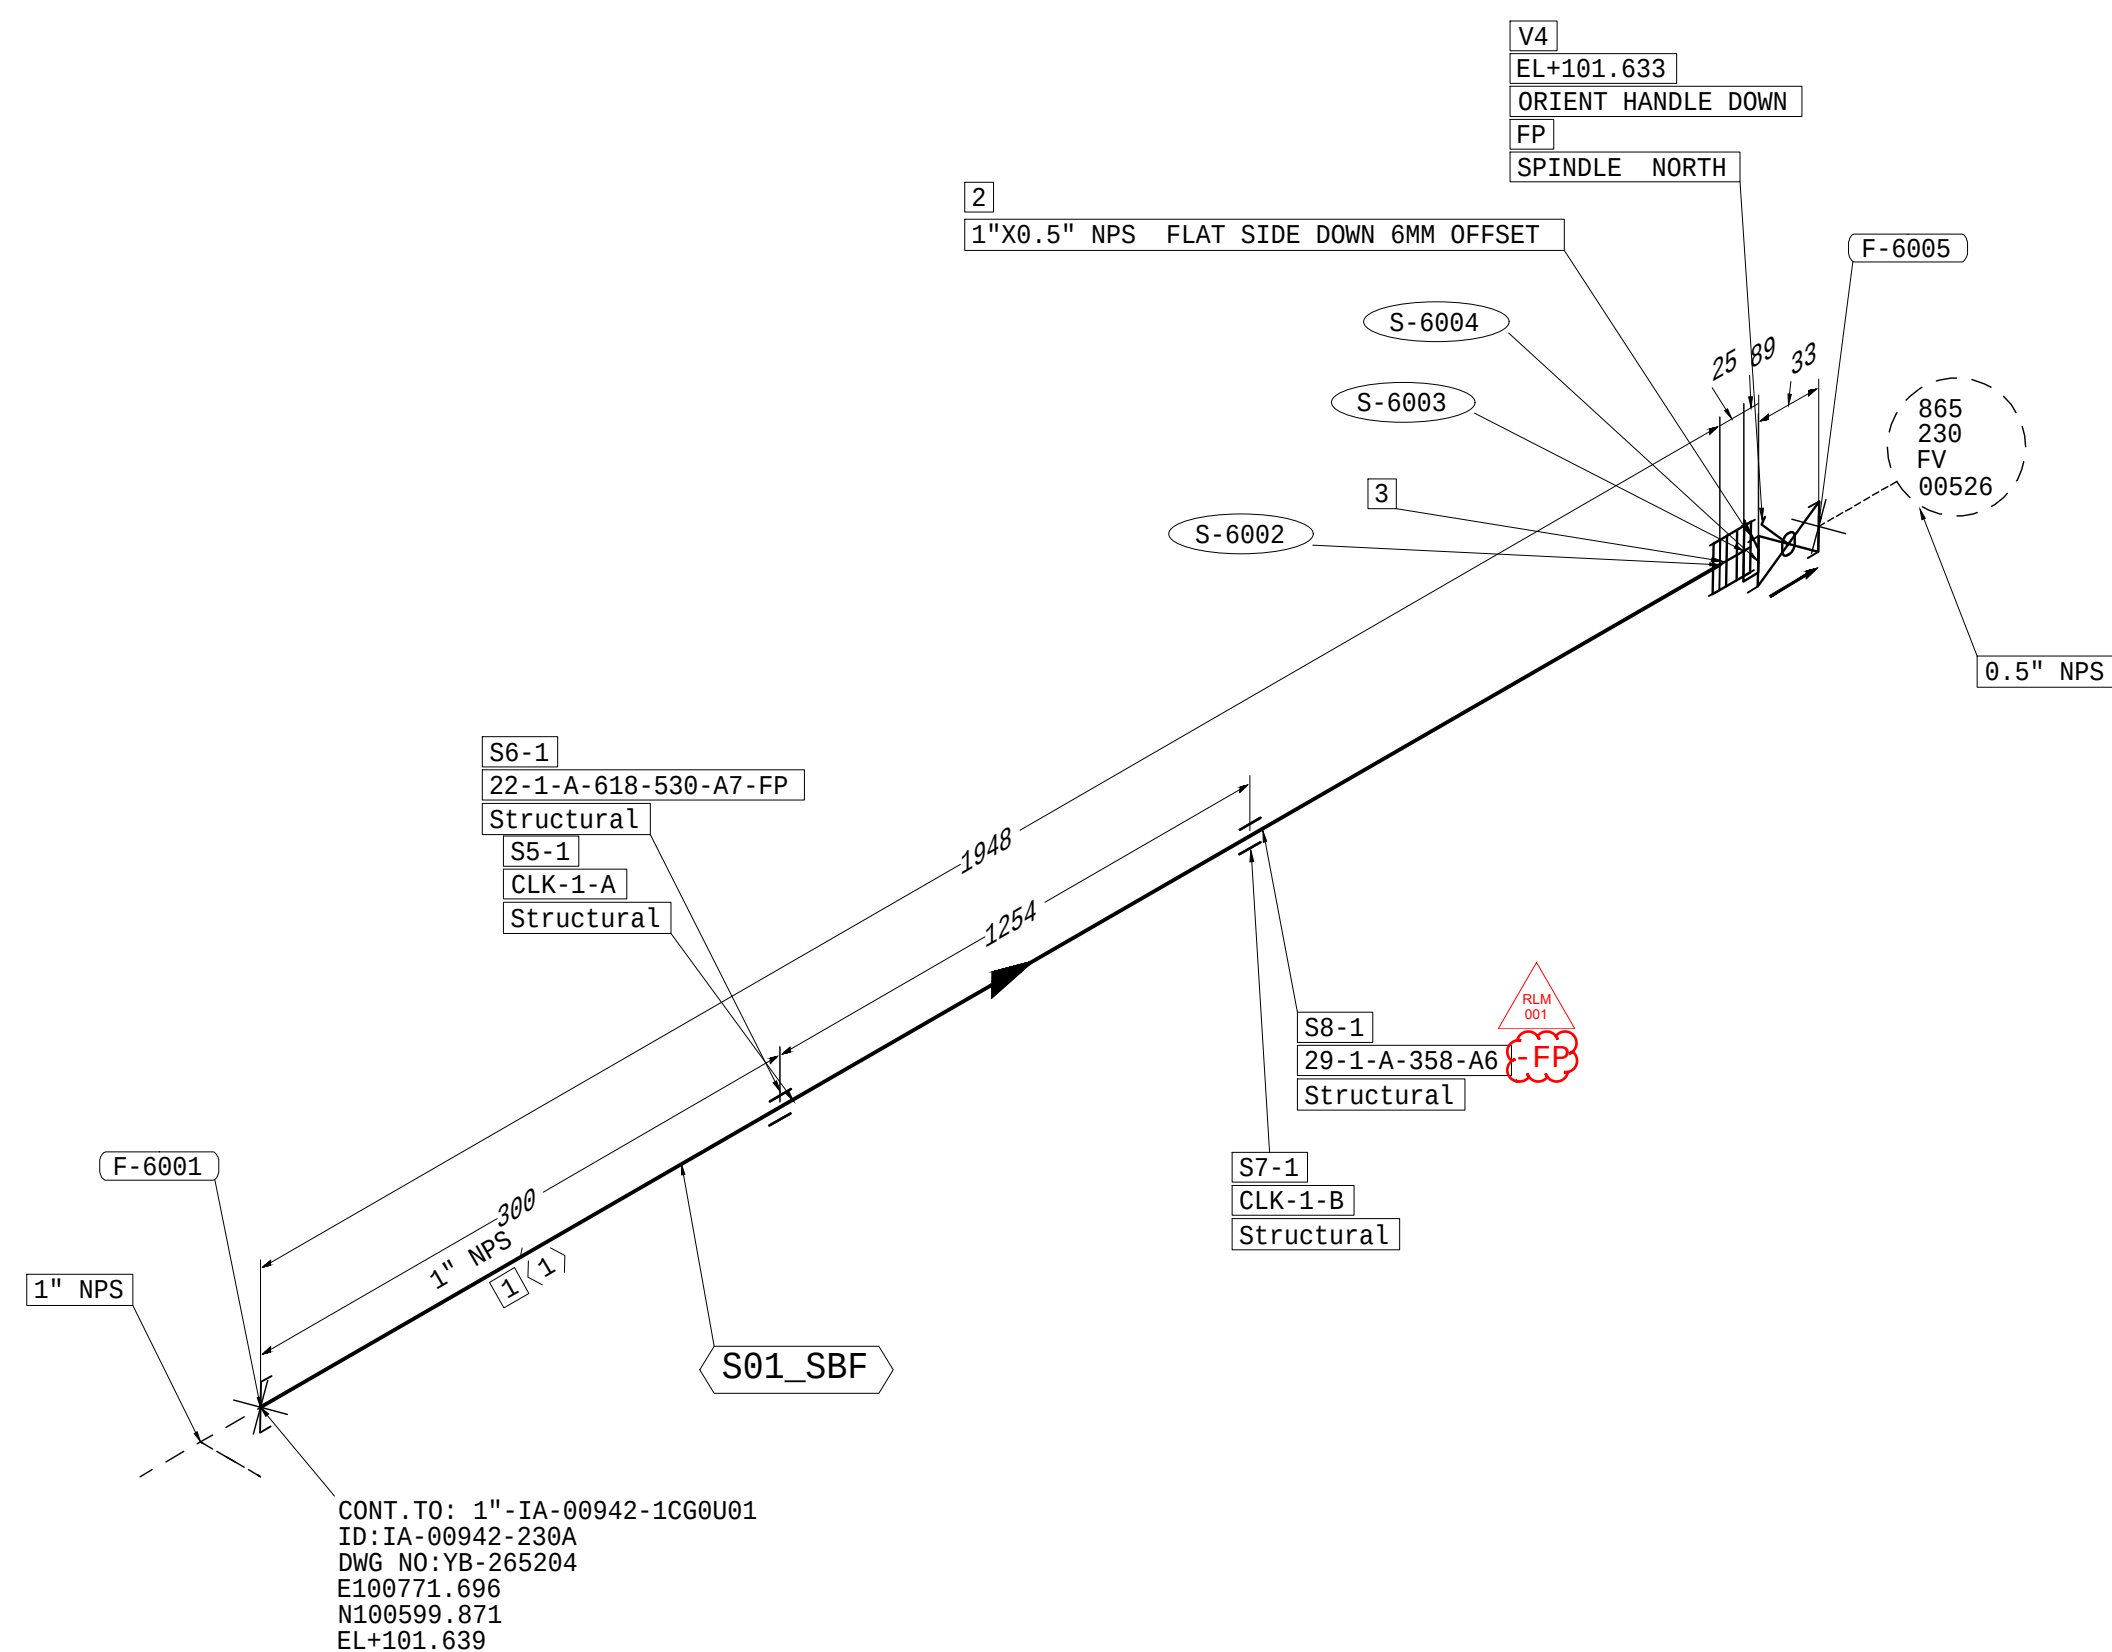


THIS IS A PRELIMINARY DRAWING. IT IS NOT TO BE USED FOR CONSTRUCTION. IT IS FOR INFORMATION ONLY. ANY DISCREPANCY IN CASE OF ANY DISCREPANCY DATA GIVEN IN ENGINEERING ISOMETRIC SHALL GOVERN.

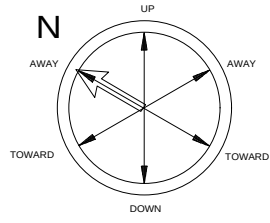

MATERIALS					STANDARD DETAIL REFERENCE DRAWINGS	
PT No.	DESCRIPTION	NPD(IN)	ITEM CODE	QTY	DETAILS HEAVY WELDING ROSSSES FOR THREADED CONNECTIONS CONSTRUCTION DETAILS AND DETAILS FOR ISOMETRIC PIPING INSULATION DETAILS FOR HOT PIPING INSULATION DETAILS FOR COLD PIPING INSTALLATION OF JACK SCREWS FOR FLANGED JOINTS	
PIPES					AE-036175 AD-036027 AA-036911 AA-036913 AC-036630	
1	PIPE SMLS 1" A106-B GALV STD NPT (M) B36.10M	1	PPS2AEAE01ZZABUUA	1.948	NOTES 1. MATERIAL SHOWN WITH A BROKEN LINE AND SPOOLS LISTED IN THE SAUDI ARAMCO FABRICATION LIST ARE NOT TO BE FURNISHED BY THE VENDOR. 2. PIPING DETAILS SHALL BE CUT AT ALL POINTS MARKED F.W. (FIELD WELD). 3. EACH FABRICATED SECTION SHALL BE CLEARLY MARKED WITH ITS CODE NUMBER. 4. UNLESS OTHERWISE NOTED: (A) ALL DIMENSIONS ARE TO FACE OF FLANGES. (B) BOLT HOLES ON FLANGES STRADDLE C. (C) WELDING ELBOWS ARE LONG RADIUS. 5. FABRICATION SHALL BE IN ACCORDANCE WITH SAUDI ARAMCO SPECIFICATION 01-SAMSS-10. 6. GASKET ALLOWANCE 7. PIPING MATERIAL IS	
FITTINGS	
2	SWG ECC 1" X 1/2" A234-WPB GALV STD NPT (M) SP-95	1X0.5	PR22AZAE01AEABUUA9	1	
3	CPLG. FULL 1" A105N GALV 3000# NPT (F) B16.11	1	PX52ADAE01ZZAA0ATA	1	
VALVE					<table><thead><tr><th>PIPE SIZE</th><th>SCHEDULE</th><th>SPECIFICATION</th></tr></thead><tbody><tr><td></td><td></td><td></td></tr><tr><td></td><td></td><td></td></tr><tr><td></td><td></td><td></td></tr></tbody></table> 8. WELDING STRESS RELIEF - YES ☐ NO ☐ 100% X-RAY ☐ SPOT X-RAY 01-SAMSS-10 ☐ 9. TESTING SHOP HYDROSTATIC TEST - YES ☐ NO ☐ THE SHOP HYDROSTATIC TEST SHALL BE CARRIED OUT ON PIECES HAVING ALL ENDS FLANGED. HYDROSTATIC TEST PRESSURE 10. ALL PIPING MATERIAL IS IN ACCORDANCE WITH SAUDI ARAMCO ENGINEERING SPECIFICATION SAES-L-105 CLASS 11. INSULATION REQUIRED - YES ☐ NO ☐ INSULATION SHOWN ON DRAWING					PIPE SIZE	SCHEDULE	SPECIFICATION	
PIPE SIZE	SCHEDULE	SPECIFICATION	
4	TAG NO V08-29-01-AS-AF-AA-BFI BALL VAL FB MSS-SP-110 1/2" B61/B62 BRONZE TRIM WITH RTFE SEAT 2/3 PIECE CONST,FLT TYP NPTF 150# LEVER OPT	0.5	V08290IAEASAFABFI	1	
SUPPORTS					<table><thead><tr><th>NO. PIECES</th><th>MARK NO.</th><th>SIZE</th><th>WEIGHT LBS</th><th>NO. PIECES</th><th>MARK NO.</th><th>SIZE</th><th>WEIGHT LBS</th></tr></thead><tbody><tr><td></td><td></td><td></td><td></td><td></td><td></td><td></td><td></td></tr><tr><td></td><td></td><td></td><td></td><td></td><td></td><td></td><td></td></tr><tr><td></td><td></td><td></td><td></td><td></td><td></td><td></td><td></td></tr></tbody></table> <table><thead><tr><th>NO. PIECES</th><th>MARK NO.</th><th>SIZE</th><th>NO. PIECES</th><th>MARK NO.</th><th>SIZE</th></tr></thead><tbody><tr><td></td><td></td><td></td><td></td><td></td><td></td></tr><tr><td></td><td></td><td></td><td></td><td></td><td></td></tr><tr><td></td><td></td><td></td><td></td><td></td><td></td></tr><tr><td></td><td></td><td></td><td></td><td></td><td></td></tr></tbody></table> REFERENCE DRAWINGS PIPING PLAN P&ID NO. YA-221234-001 PLOT PLAN KEY PLAN NO. TA-293108 INDEX FOR PIPING ISO (AG) PP-865-LI-0003 INDEX FOR PIPING ISO (UG) PP-865-LI-0004 <table><thead><tr><th>REV</th><th>DATE</th><th>DESCRIPTION</th><th>PROD BY</th><th>CHKD BY</th><th>APP BY</th><th>APP BY</th></tr></thead><tbody><tr><td>00</td><td>29-09-25</td><td>ISSUED FOR CONSTRUCTION</td><td>AC/SN</td><td>KY/PD</td><td>BSP</td><td>HJ</td></tr></tbody></table> REVISION STATUS THIS REVISION NO 00 IS COVERED, FOR ALL APPROVAL AND CERTIFICATION REQUIREMENTS, PER SAEP-33A, UNDER DRAWING COMPLETION CERTIFICATE NO: 10-14815-0003-000 <table><thead><tr><th colspan="2">DESIGN CERTIFICATION (DESIGN AGENCY'S)</th><th colspan="2">REVIEW FOR KEY DRAWINGS (SAUDI ARAMCO)</th><th colspan="2">OTHER</th></tr><tr><th>ENGG./DATE</th><th>CERTIFIED BY/DATE</th><th>CONST. AGENCY/DATE</th><th>OPERATIONS/DATE</th><th>BY/DATE</th><th></th></tr></thead><tbody><tr><td></td><td></td><td></td><td></td><td></td><td></td></tr></tbody></table> JOB ORDER/REV NO. 10-14815-0003 THIS REVISION IS NOT TO BE USED FOR CONSTRUCTION UNLESS CERTIFIED AND DATED SAUDI ARABIAN OIL COMPANY ISOM 1" -IA-00944-1CG0U01 IA SERVICE JFGP GAS PROCESSING TRAIN-2 JAFURAH SAUDI ARABIA PLANT NO. 865 INDEX L DRAWING NUMBER YB-265205 SHT. NO. 010f01 REV. NO. 00 SITE REV. NO. 001 RESTRICTED SMART CADD-03					NO. PIECES	MARK NO.	SIZE	WEIGHT LBS	NO. PIECES	MARK NO.	SIZE	WEIGHT LBS																									NO. PIECES	MARK NO.	SIZE	NO. PIECES	MARK NO.	SIZE																									REV	DATE	DESCRIPTION	PROD BY	CHKD BY	APP BY	APP BY	00	29-09-25	ISSUED FOR CONSTRUCTION	AC/SN	KY/PD	BSP	HJ	DESIGN CERTIFICATION (DESIGN AGENCY'S)		REVIEW FOR KEY DRAWINGS (SAUDI ARAMCO)		OTHER		ENGG./DATE	CERTIFIED BY/DATE	CONST. AGENCY/DATE	OPERATIONS/DATE	BY/DATE							
NO. PIECES	MARK NO.	SIZE	WEIGHT LBS	NO. PIECES						MARK NO.	SIZE	WEIGHT LBS	
NO. PIECES	MARK NO.	SIZE	NO. PIECES	MARK NO.	SIZE	
REV	DATE	DESCRIPTION	PROD BY	CHKD BY	APP BY	APP BY	
00	29-09-25	ISSUED FOR CONSTRUCTION	AC/SN	KY/PD	BSP	HJ	
DESIGN CERTIFICATION (DESIGN AGENCY'S)		REVIEW FOR KEY DRAWINGS (SAUDI ARAMCO)		OTHER	
ENGG./DATE	CERTIFIED BY/DATE	CONST. AGENCY/DATE	OPERATIONS/DATE	BY/DATE	
5	PIPE SUPPORT	1	CLK-1-A	1	
6	PIPE SUPPORT	1	22-1-A-618-530-A7-FP	1	
7	PIPE SUPPORT	1	CLK-1-B	1	
8	PIPE SUPPORT	1	29-1-A-358-A6	1	

PIPE CUT LENGTH SUMMARY					ISO For					
SPL No.	NPD	PC No.	LENGTH	ALLOWANCE	TOTAL LENGTH	SXX_Spool Sequence Number (S01,02, SXX_SF - Fab. Spool SXX_SF - Fab. P to P Doubling (0-6M/0-4 SXX_SF - Erec. Random Pipe (0M,12M) SXX_SF - Erec. Part Loose Fittings SXX_SF - Erec. Flange (F-Loose Flange, FTS-Basic, FTS-Speciality) SXX_EV - Erec. valve SXX_EPG - Erec. Pipe Plug SXX_SBF - Small Bore Spool Fab. SXX_SBE - Small Bore Spool Erec. SXX_SBD - Small Bore Spool Drain SXX_SBV - Small Bore Spool Vent				
S01_SBF	1	<1>	1.948	0.000	1.948	PART NUMBER PIECE NUMBER SHOP WELD FIELD WELD SPOOL NUMBER				

NOTES :														
1. ALL COORDINATES AND ELEVATIONS ARE IN 'METER' AND ALL DIMENSIONS ARE IN 'MM'. 2. PIPE QUANTITY IS IN METERS AND OTHER QUANTITY IN NUMBERS. 3. FOR STANDARD SUPPORT, REFER DOC. NO. "PP-866-ST-0001" 4. IN CASE OF ANY DISCREPANCY FOR LINE CONDITIONS, LINE DATA GIVEN IN LINE LIST SHALL GOVERN 5. FOR SMALL BORE LINES, DIMENSION & ROUTING SHALL BE FIELD ADJUSTED. 6. THE SPECIFIED THEORETICAL LOCATION OF EQUIPMENT NOZZLES, SUPPORTING STRUCTURE SHALL BE VERIFIED BEFORE INSTALLING THE PIPING & INTOLERABLE DISCREPANCIES SHALL BE DISCUSSED WITH DESIGN SITE ENGINEER. 7. ALL THREADED CONNECTION SHALL BE SEAL WELDED, EXCEPT DRAIN AND VENT PLUG. 8. REFER LINE LIST. 9. ALL PRESSURE WELDS, OTHER THAN BUTT WELDS, INCLUDING BRANCH CONNECTIONS SUCH AS BRANCH-OLETS, AND BOSS) SHALL BE 100% PTMT EXAMINED. ALL ATTACHMENT WELDS ON PRESSURIZED COMPONENTS THAT ARE NOT HYDROTESTED AFTER MAKING THE ATTACHMENT WELD SHALL BE 100% PTMT EXAMINED.														

BUTT WELD		FIELD WELD	
INSULATED PIPE	TRACED PIPE	PIPE SUPPORT	PLATFORM PENETRATION
SOCKET WELD	SCREWED JOINT		

DESIGN		OPERATING		TEST PRESS. (PSIG)	TEST MEDIUM	RADIOGRAPHY %	INSULATION		TRACING	PAINTING	STRESS SYS NO.	LINE ID
TEMP. (DEG. F)	PRESS. (PSIG)	TEMP. (DEG. F)	PRESS. (PSIG)				THK. (MM)	TYPE				
185	145	135	125	125	SERVICE	NA	NA	0	NI	NA	APCS-26	IA-00944-230A

PWHT	CHEMICAL CLEANING	PIPING MATERIAL CLASS	DESIGN	OPERATING	TEST PRESS. (PSIG)	TEST MEDIUM	RADIOGRAPHY %	INSULATION	TRACING	PAINTING	STRESS SYS NO.	LINE ID
N	NOTE-8	1CG0U01	185	145	135	125	SERVICE	NA	NA	0	NI	IA-00944-230A

NOTES CONT. :
91. FOR SOUR SERVICE PWHT IS MANDATORY FOR 1. DOUBLE SIDED WELDING, 2. INTERNAL WELD REPAIR 3. INTERNAL WELD BUILD UP FOR DISSIMILAR THICKNESS JOINTS TO OVERCOME MISALIGNMENT.

All Pipe attached supports shall be welded before galvanising.

450437 09-02-2026

450444 21-04-2026