


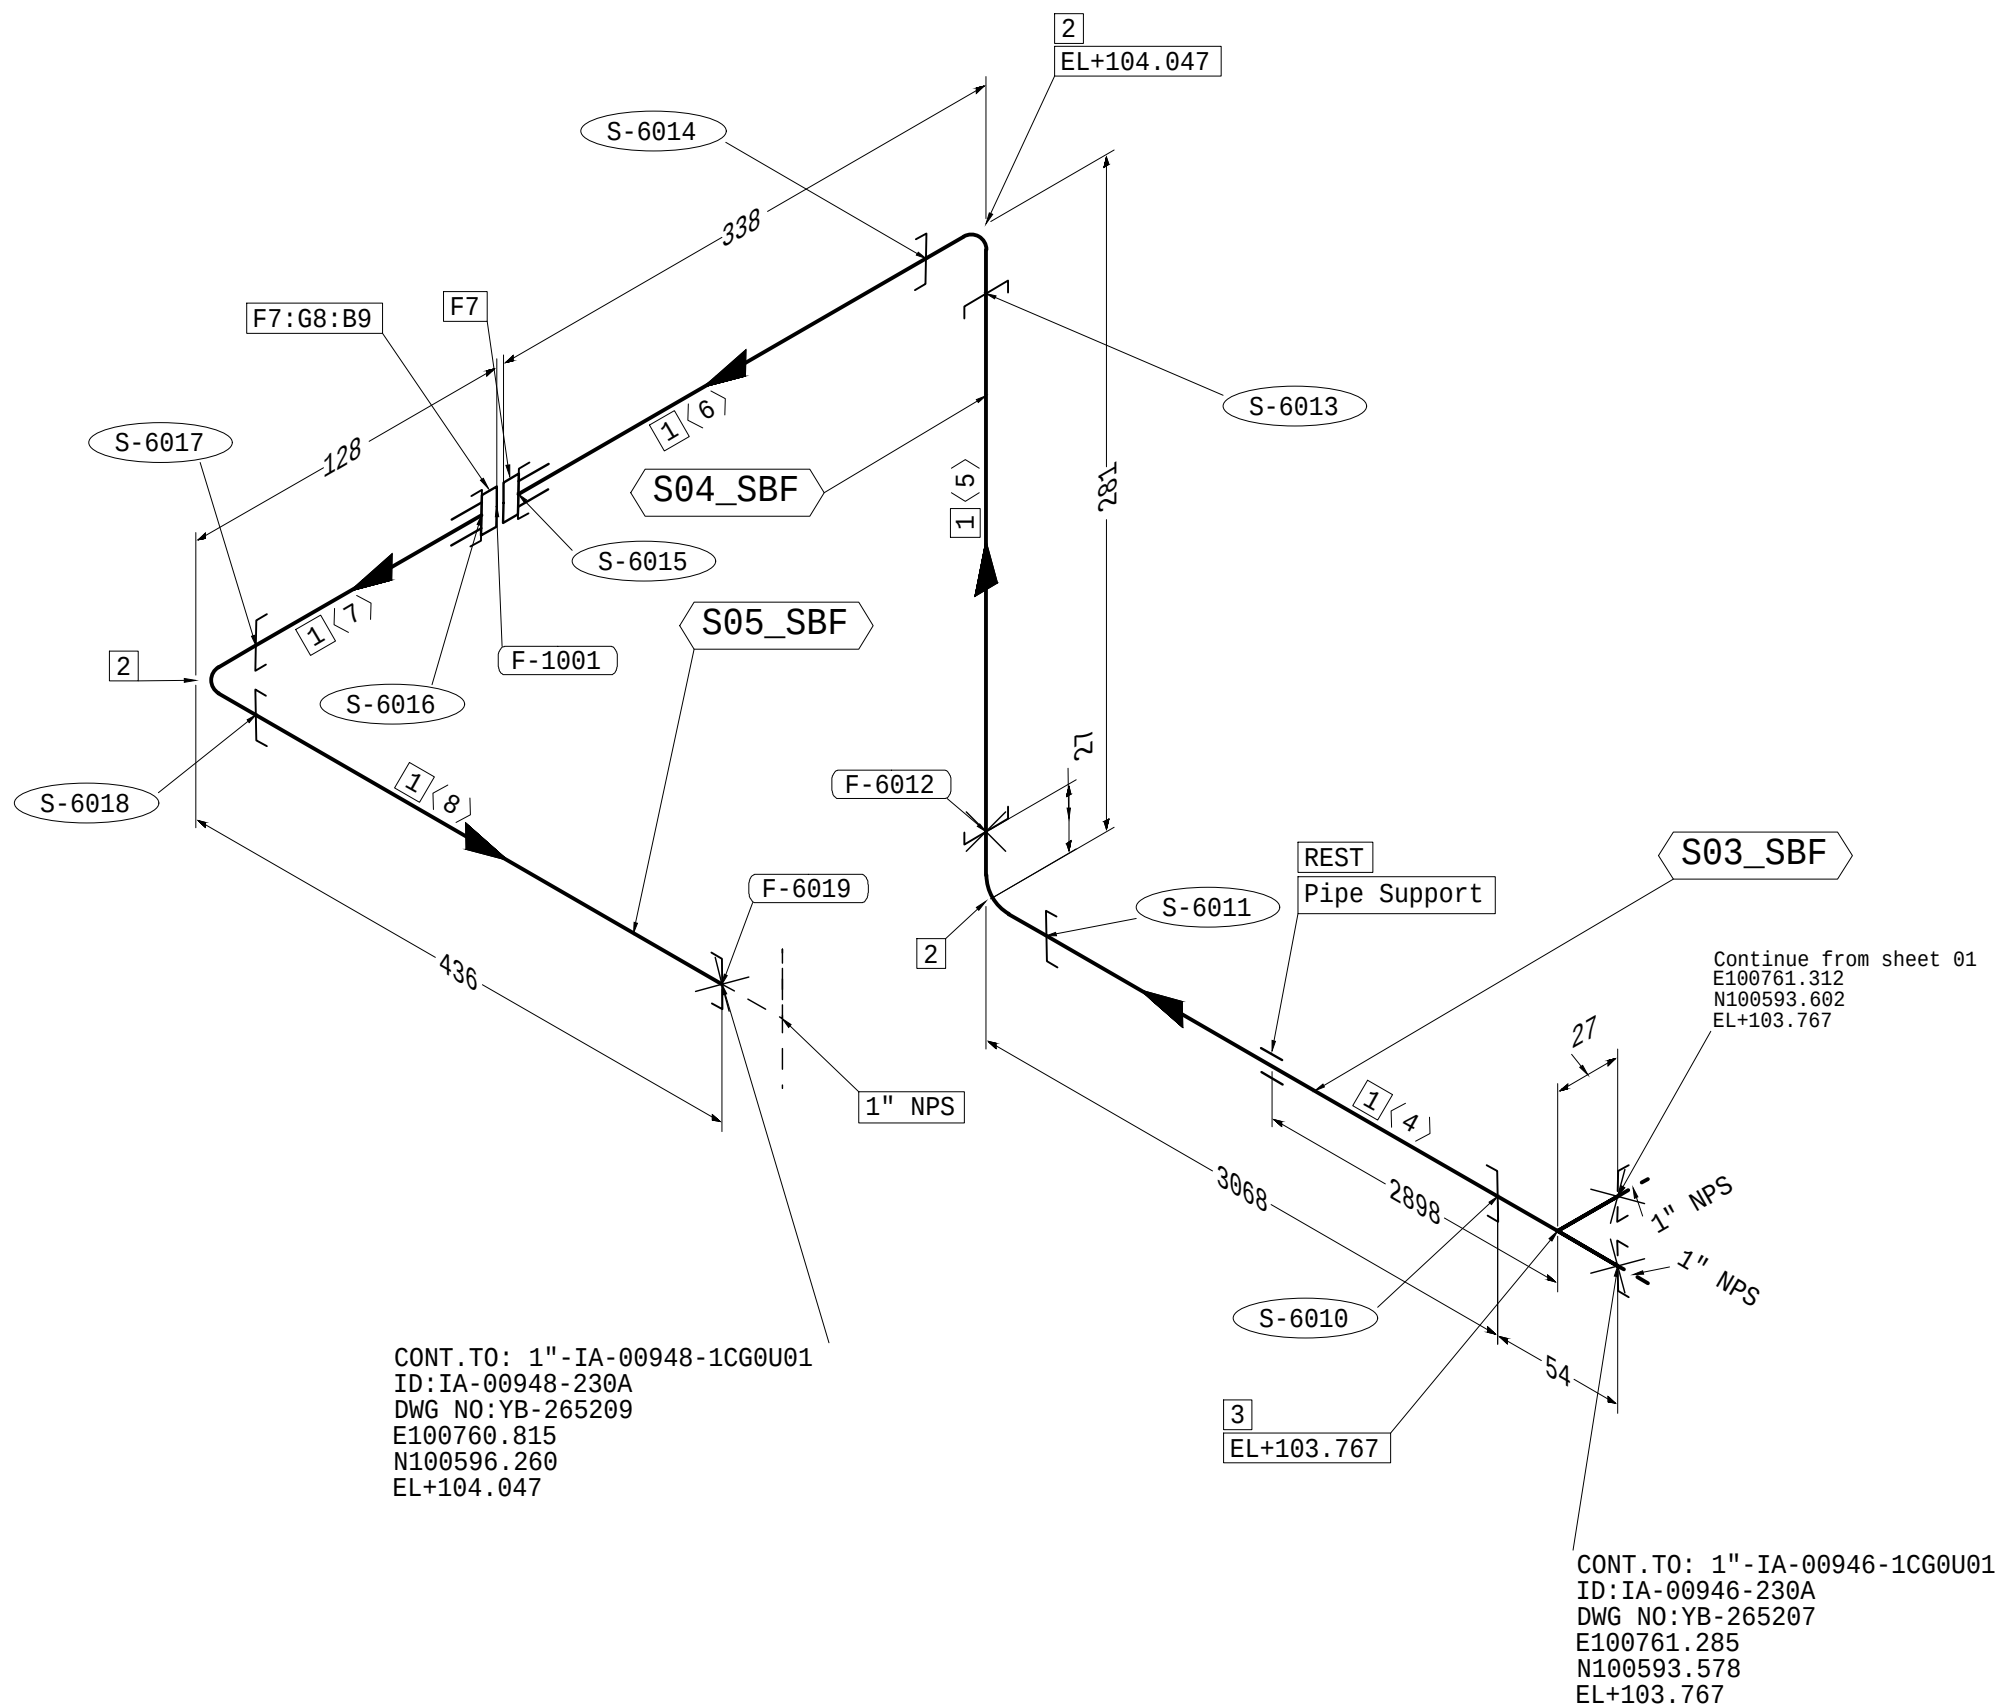

CONT.TO: 1"-IA-00946-1CG0U01
ID:IA-00946-230A
DWG NO:YB-265207
E100761.285
N100593.578
EL+103.767

NOTES CONT. :

91. FOR SOUR SERVICE PWHT IS MANDATORY FOR 1. DOUBLE SIDED WELDING, 2. INTERNAL WELD REPAIR 3. INTERNAL WELD BUILD UP FOR DISSIMILAR THICKNESS JOINTS TO OVERCOME MISALIGNMENT.

[illegible]

Saudi Aramco 2825 ENG. (05/05)

RESTRICTED	SMART	CADD-03
------------	-------	---------

RESTRICTED SMART CADD-03